




PLANTA ESCALERA 1°PISO a 2°PISO
ESCALA 1:50

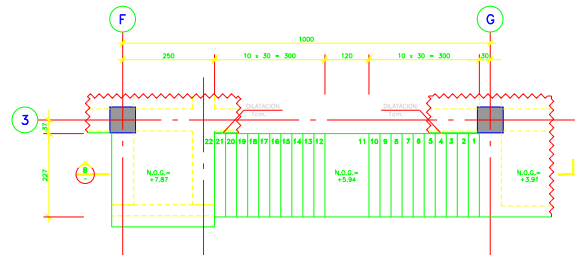


PLANTA ESCALERA 2°PISO a 3°PISO
ESCALA 1:50

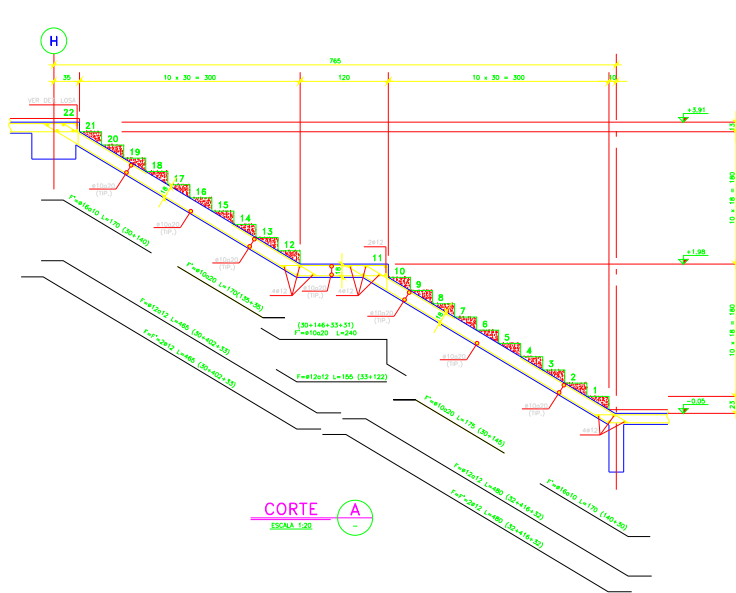


CORTE A
ESCALA 1:20

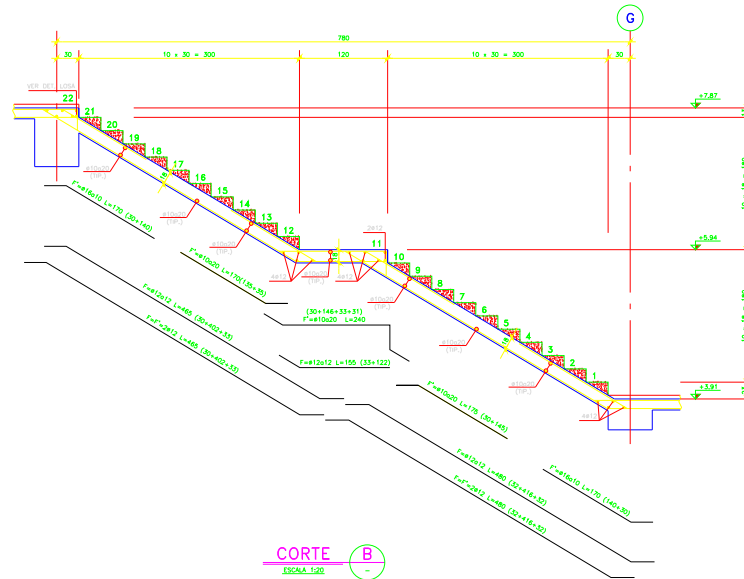

CORTE B
ESCALA 1:20

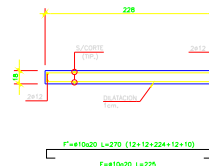

CORTE H
ESCALA 1:20

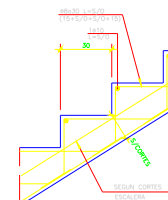

DETALLE ALTERNATIVO
GRADAS ARMADAS
ESCALA 1:10

ESTADO:		APROBADO PARA:		MAGDALENA 140 PIR 24 OF 2405 LAS COMEDAS	
EN DESARROLLO	PRELIMINAR	PROPIETARIA	CONSTRICCION	SANTOAGO, CHILE FONOS: +56 9 38841300	reinelagos
REVISOR	REVISOR	REVISOR	REVISOR	info@reinelagos.com www.reinelagos.com	
FECHA PARA PROYECTO	20/10/2021	FECHA	21/10/2021	PROYECTO	U. DE LOS ANDES
				DETALLE DE ESCALERAS	