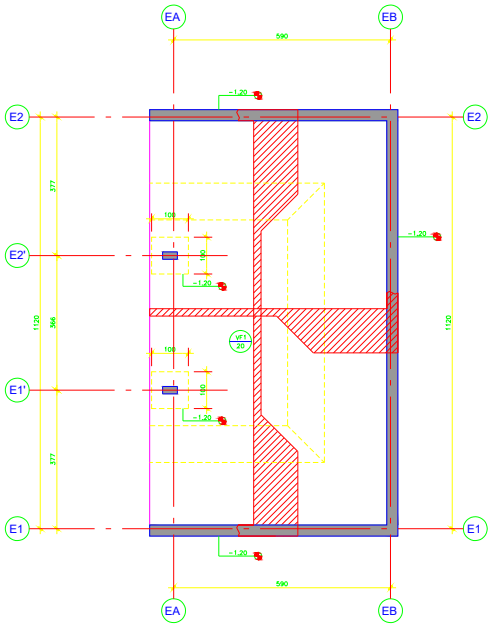

PLANTA FUNDACIONES
ESCALA 1:50

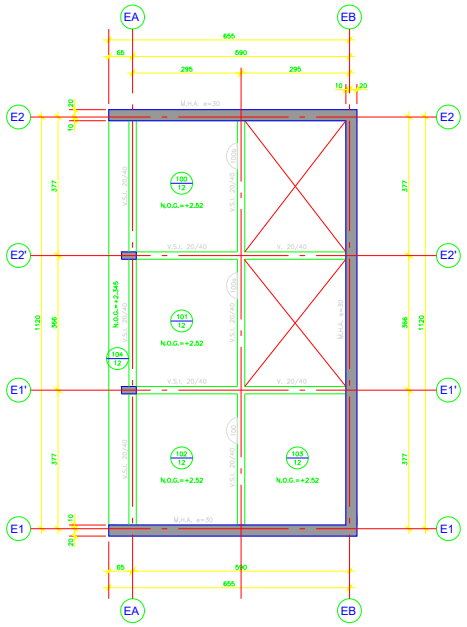

PLANTA CIELO 1° PISO
ESCALA 1:50

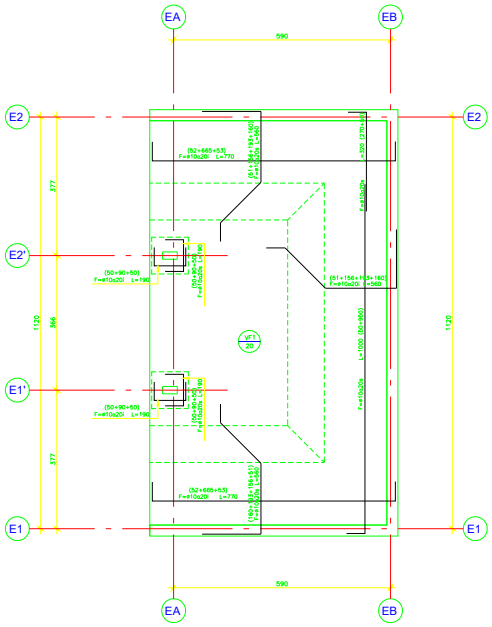

PLANTA LOSA FUNDACIONES
ESCALA 1:50

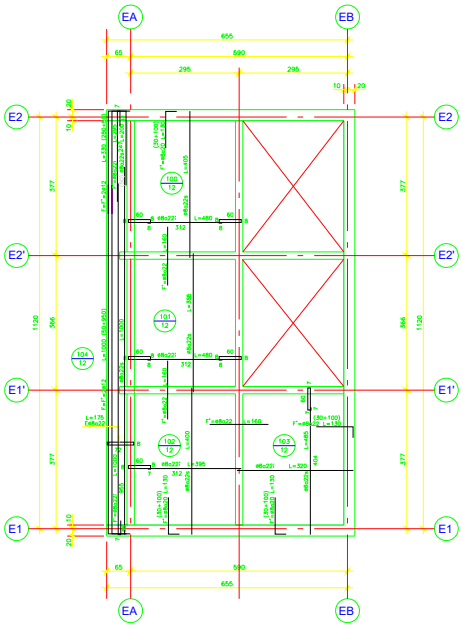

PLANTA LOSA CIELO 1° PISO
ESCALA 1:50

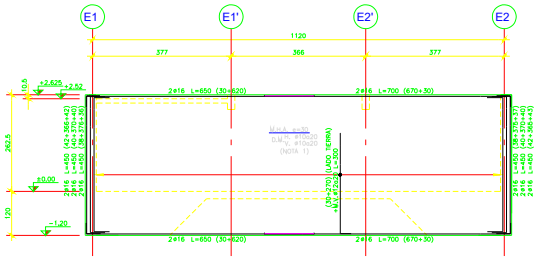

ELEVACION EJE EB
ESCALA 1:50

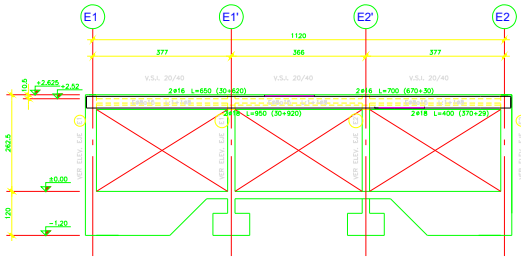

ELEVACION EJE EA
ESCALA 1:50

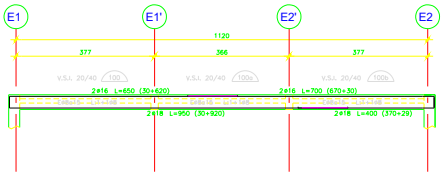

NOTA 1:
VER DET. DE DISPOSICION DE MALLAS EN MURO DE CONTENCION EN PLANO N° 001

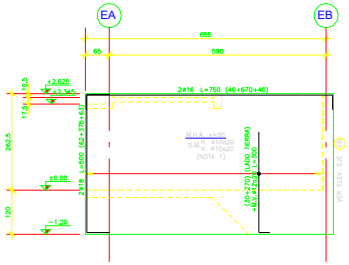

ELEVACION EJE E2
ESCALA 1:50

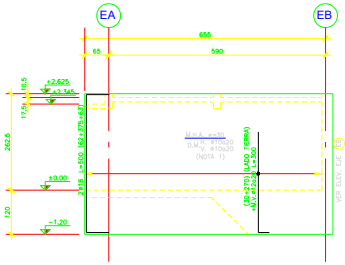

ELEVACION EJE E1
ESCALA 1:50

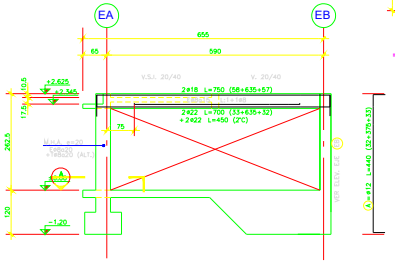

ELEVACION EJE E2' = E1'
ESCALA 1:50

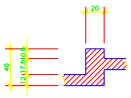

V.S.I. 20/40
ESCALA 1:20

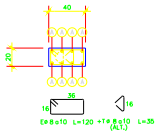

CORTE A
ESCALA 1:20

MATERIALES

HORMIGÓN G25_10:

-RESISTENCIA A COMPRESIÓN PROBETA CILÍNDRICA FC' = 25 MPA, EQUIVALENTE A RESISTENCIA A COMPRESIÓN PROBETA CÚBICA R28 = 30 MPA Y 90% NC

-TAMAÑO MÁXIMO DE ÁRIDO Y ASENTAMIENTO DE CONO DEBERÁN SER DEFINIDOS POR LA CONSTRUCTORA DE MODO DE GARANTIZAR EL CORRECTO HORMIGONADO DE LOS ELEMENTOS.

-LA COMPOSICION DEL HORMIGON DEBERA CONSIDERAR LOS PARAMETROS DE DURABILIDAD ESTABLECIDOS EN NCh170:2016. LOS GRADOS DE EXPOSICION DEBERAN SER DEFINIDOS POR UN ESPECIALISTA EN MATERIA DE HORMIGONES, DE ACUERDO A:

- EMPLAZAMIENTO Y ENTORNO
- TIPO DE EXPOSICIÓN
- USO DE MEDIDAS ESPECIALES DE PROTECCIÓN
- EXISTENCIA DE ESTUDIOS ESPECIALES

A FALTA DE ESPECIALISTA SE DEBE CONSIDERAR LAS CONDICIONES MAS SEVERAS ESTABLECIDAS EN NCh170:2016.

EN CASO QUE SE REQUIERA, POR CONDICIONES DE DURABILIDAD, UN HORMIGON DE GRADO SUPERIOR AL ESPECIFICADO, ESTO DEBE SER INFORMADO A RLE.

ACERO A630-420H

ESTADO:		APROBADO PARA:	
EN DESARROLLO	PRELIMINAR	PROPUESTA X	CONSTRUCCION

N°	REVISION	ING. / DIB.	FECHA
A	SE EMITE PARA PROPUESTA	JAC/EMF	22/02/2018

MAGDALENA 140 Piso 24 OF.2402 LAS CONDES
SANTIAGO, CHILE | FONO: +56 2 25841300
info@renelagos.com | www.renelagos.com

renelagos
engineers

PROYECTO
U. DE LOS ANDES

CONTENIDO
DETALLE SALA ELECTRICA

ESTE LAGOS CONSTRUYE NUESTRAS CONFIANZAS CON EL CONTENIDO DE ESTE DOCUMENTO. LAS DE LA FUENTE ENTRE SIGUEN SIENDO TERRENOS.

CALCULO	DIBUJO	ESCALAS	NUMERO	REV.
MOLINA C.	MORALES	1:50	2017_67-600	A
DISEÑO	REVISO	FECHA		
C. MORALES F.	P. RUPERT C.	DICIEMBRE 2017		

2017_67-600.dwg
Fr. 28 Jan 2018 10:51:11am