



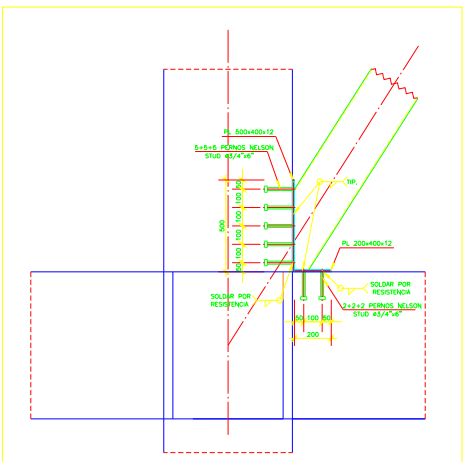

DETALLE 2  
ESCALA 1:10

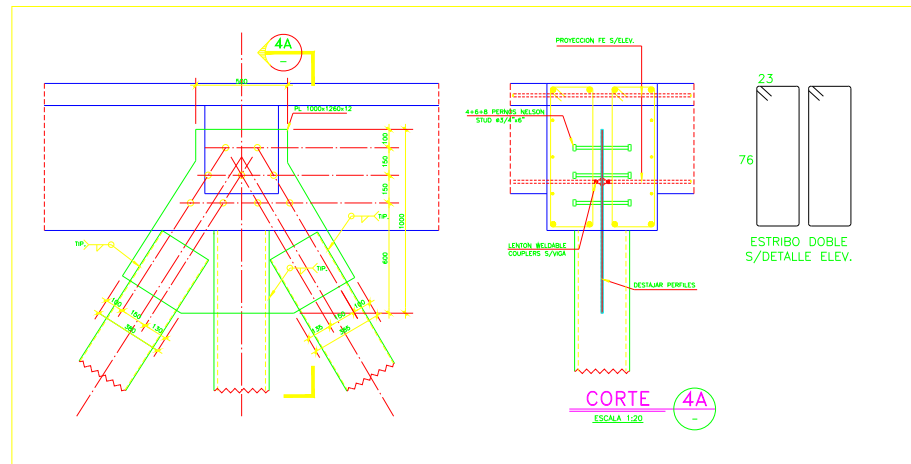

DETALLE 4

ESCALA 1:10

|   |                        |                        |              |   |  |
|---|------------------------|------------------------|--------------|---|--|
| <b>ESTADO:</b>   |                        | <b>APROBADO PAÑA:</b>  |              |                                        |  |
| EN DESARROLLO [PENDIENTE]   |                        | PROPUESTA Y CONEXIONES |              | MADRILENA 140 Pina 24 Of.5405 LAS CONDES<br>MADRILENA, C/DEL E FOMU -68 1.2004200<br>info@renelagos.com   www.renelagos.com |  |
| <b>Nº</b>   | <b>VERSION</b>         | <b>IMP./OBL.</b>       | <b>FECHA</b> |   |  |
| 1   | SE EMITE PARA PROYECTA | IMP./OBL.              | 22/12/2017   |   |  |
|   |                        |                        |              | <b>PROYECTO</b><br><b>U. DE LOS ANDES</b><br><b>DETALLES DE CONEXIONES</b><br><b>METALICAS EJE 1-2-3</b>                    |  |
| Este es un documento de trabajo<br>con fines de consulta<br>No debe ser utilizado para<br>emitir ni aceptar ni<br>firmar ni aceptar ni<br>firmar ni aceptar ni |                        |                        |              |   |  |
| <b>FECHA</b>   | <b>IMPRESOR</b>        | <b>REVISOR</b>         | <b>FECHA</b> |   |  |
| 2017_67-800 A   |                        |                        |              |   |  |