



DETALLES TÍPICOS DE ARMADO DE MUROS CON CONFINAMIENTO (SALVO INDICACIÓN CONTRARIA)

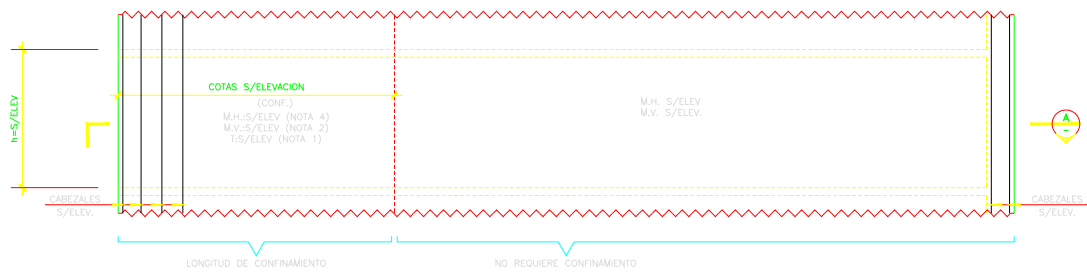


ELEVACIÓN MURO

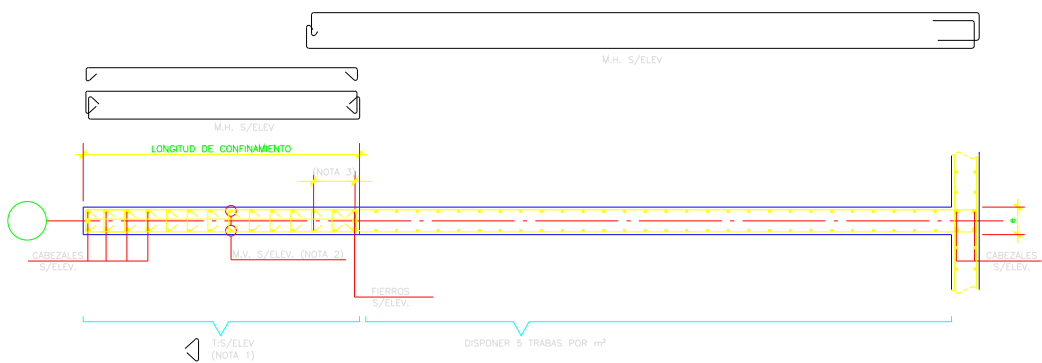


CORTE A

DETALLE TÍPICO DE CONFINAMIENTO CON MALLAS EN PUNTAS DE MURO

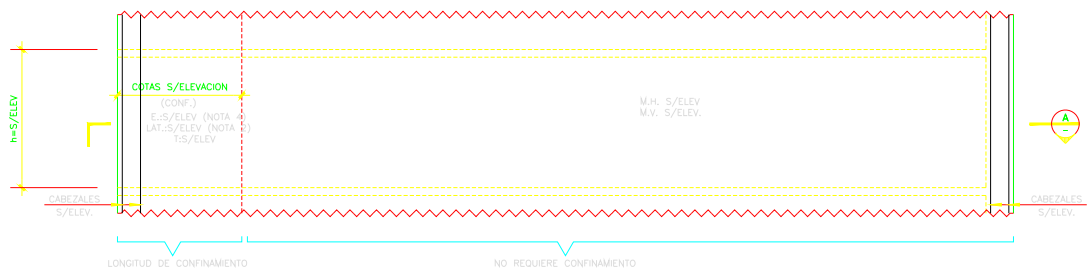

ELEVACIÓN MURO

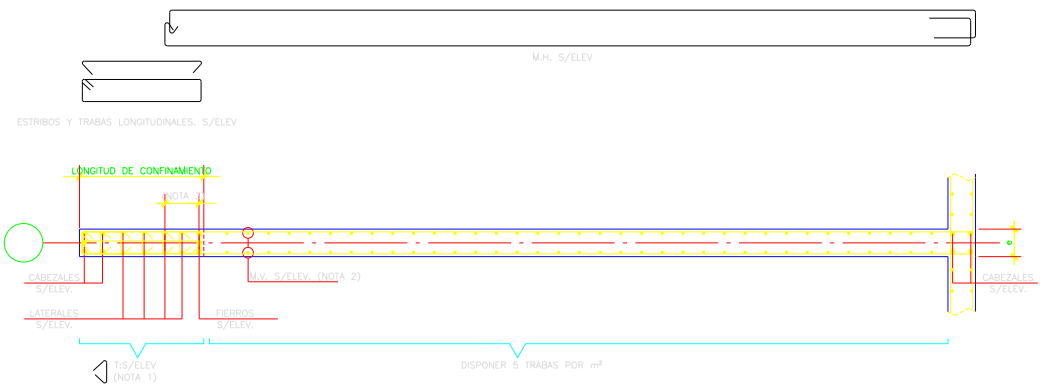


CORTE A

DETALLE TÍPICO DE CONFINAMIENTO CON ESTRIBOS Y LATERALES EN PUNTAS DE MURO

NOTAS:

- (1) Las barras de confinamiento (V o C/H): LAS TRABAS DE BARRAS VERTICALES UBICADAS DENTRO DE LA LONGITUD DE CONFINAMIENTO, TENDRÁN DIÁMETRO "A", SE DEBERÁN DISPONER ESPACIADAS A "B" CM EN VERTICAL Y A "C" CM EN HORIZONTAL.
- (2) LA MALLA VERTICAL O LATERALES UBICADOS EN LA ZONA DE CONFINAMIENTO SE TRASLAPARÁ PISO A PISO CON LA SIGUIENTE LONGITUD DE EMPALME DEPENDIENDO DEL DIÁMETRO DE LA BARRA:
#16 → EMPALMES 130cm
#18 → EMPALMES 140cm

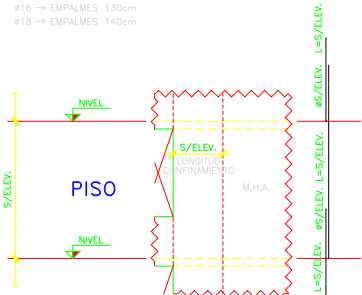

ELEVACIÓN MURO

- (3) EL EMPALME ENTRE LA MALLA HORIZONTAL Y LA MALLA O ESTRIBO DE CONFINAMIENTO DEBERÁ SER COMO MÍNIMO DE 30cm DENTRO DEL ÁREA CONFINADA PARA MALLA HORIZONTAL DE DIÁMETRO MENOR O IGUAL A #18. PARA DIÁMETROS MAYORES A #18 EL EMPALME DEBERÁ SER DE MÍNIMO 45cm




- (4) LAS MALLAS HORIZONTALES DEBERÁN TENER EN AMBOS EXTREMOS UN DOBLEZ EN 90° Y OTRO EN 135°. LOS ESTRIBOS DEBERÁN TENER DOS DOBLECES EN 135°.




AMBAS ALTERNATIVAS SON VÁLIDAS PARA DAR CONFINAMIENTO

- (5) LOS ESTRIBOS Y TRABAS DE CONFINAMIENTO (O MALLAS DE CONFINAMIENTO) DEBERÁN PENETRAR 30cm EN LAS FUNDACIONES.

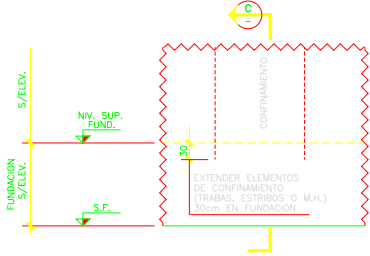


DETALLE TIP. INICIO DE CONFINAMIENTO EN FUNDACIÓN

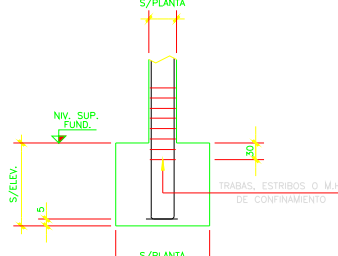

CORTE C

- (6) EN CASO DE DETALLARSE EN ELEVACIÓN "TRABA ALT. C/R A MALLA HORIZONTAL", SE DEBERÁN DISPONER LAS TRABAS DE ACUERDO AL SIGUIENTE ESQUEMA.

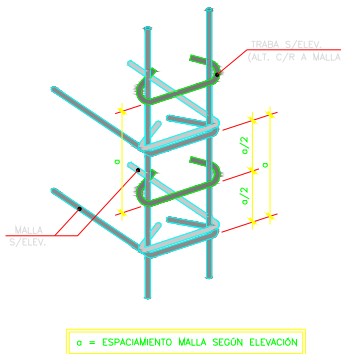

DETALLE TIP. CASO TRABAS ALT. C/R A MALLA

ESTADO:				APROBADO PARA:			
EN DESARROLLO	PRELIMINAR	PROPUESTA	X	CONSTRUCCIÓN			
REVISIÓN				ING. / DIB.	FECHA		
A	SE EMITE PARA PROPUESTA			JMC/CM	22/02/2018		

MAGDALENA 140 Piso 24 OF.2402 LAS CONDES SANTIAGO, CHILE FONDO: +56 2 25841300 info@renelagos.com www.renelagos.com				renelagos engineers			
PROYECTO				U. DE LOS ANDES			
CONTENIDO				PLANO DE DETALLES TÍPICOS			
RENE LABOS CONTRERAS MAHNE GUZMÁN CAUPE GUZMÁN AMAR ESPARZA LUIS DE LA FUENTE MARTÍNEZ SHIRY SARRIENZA TORREALBA				CÁLCULO: RENE LABOS CONTRERAS DISEÑO: MAHNE GUZMÁN CAUPE REVISIÓN: GUZMÁN AMAR ESPARZA DIBUJO: SHIRY SARRIENZA TORREALBA			
Escala: 1:100cm		Escala: 1:100cm		Escala: 1:100cm		Escala: 1:100cm	
FECHA: 2017_07-01		FECHA: 2017_07-01		FECHA: 2017_07-01		FECHA: 2017_07-01	
NÚMERO: 2017_67-001		NÚMERO: 2017_67-001		NÚMERO: 2017_67-001		NÚMERO: 2017_67-001	