DET. 1

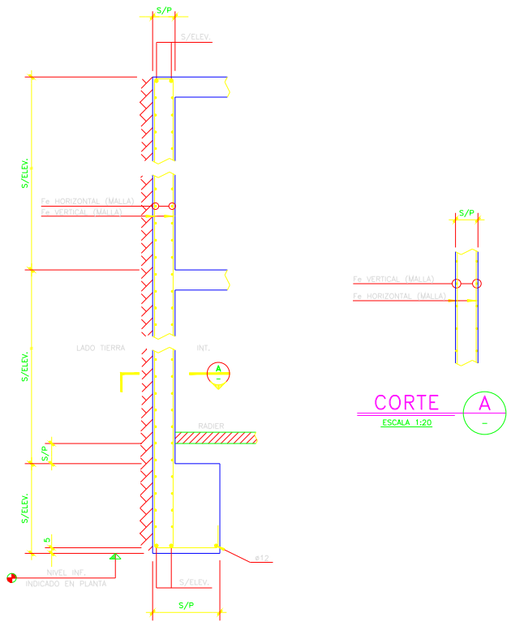

CORTE A
ESCALA 1:20

DISPOSICION DE ARMADURAS EN MURO CONTENCION
ESCALA 1:20

DET. 2

CASO 1: MURO LEVEMENTE INTERRUMPIDO POR PILA

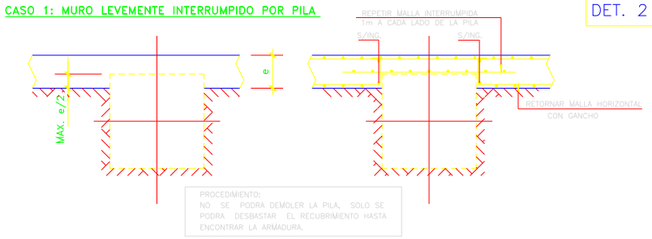

PROCEDIMIENTO:
NO SE PODRA DEMOLER LA PILA, SOLO SE PODRA DESBASTAR EL RECUBRIMIENTO HASTA ENCONTRAR LA ARMADURA.

CASO 2: MURO PARCIALMENTE INTERRUMPIDO POR PILA

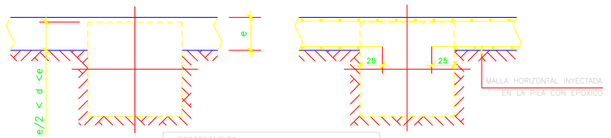

PROCEDIMIENTO:
NO SE PODRA DEMOLER LA PILA, SOLO SE PODRA DESBASTAR EL RECUBRIMIENTO HASTA ENCONTRAR LA ARMADURA.

CASO 3: MURO TOTALMENTE INTERRUMPIDO POR PILA

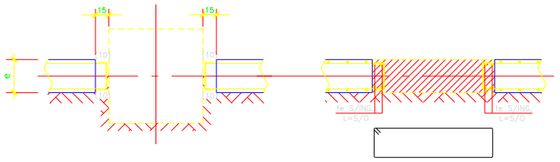

PROCEDIMIENTO:
1.- HORMIGONAR EL MURO DEJANDO UNA FRANJA SIN HORMIGONAR DE 15 cm A AMBOS LADOS DE LA PILA. DISPONER LA MALLA HORIZONTAL CON LOS GANCHOS INDICADOS EN EL DIBUJO.
2.- UNA VEZ HORMIGONADA LA LOSA Y DESTENSADA LA PILA, DEMOLER LA PILA Y HORMIGONAR EL RESTO DEL MURO, COLOCAR ESTRIBO HORIZONTAL CON EL MISMO DIAMETRO Y ESPACIAMIENTO DE LA MALLA VERTICAL RESPECTIVA.

DETALLES PARA EJECUCION DE MUROS DE CONTENCION INTERRUMPIDOS POR PILAS DE SOCALZADO
ESCALA 1:25

DET. 3

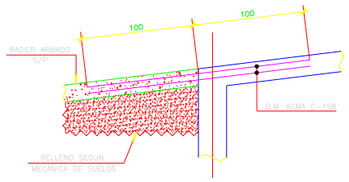

DETALLE ENCUENTRO LOSA RAMPA CON RADIER EN RELLENO
ESCALA 1:20

DET. 4

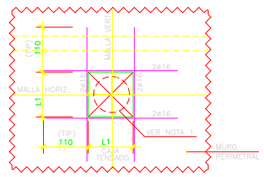

NOTA 1= LAS MALLAS DEBEN CORTARSE, DOBLARSE Y LUEGO COLOCAR 1+1ø IGUAL DIAMETRO QUE LA MALLA VERTICAL Y HORIZONTAL LARGO SEGUN L1, CUANDO SE TERMINE DE HORMIGONAR MURO PERIMETRAL.
L1=ANCHO DE LA CAJA DE TENSADO +ANCHO MAX. 40x40 cm.

(TAMAÑO MAX. 40x40 cm.)

DETALLE TIP REFUERZO CAJA DE TENSADO
ESCALA 1:25

DET. 5

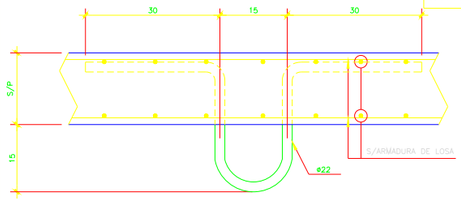

DETALLE GANCHO DE ASCENSOR EN Llosa
ESCALA 1:5

DET. 6

NOTA: EN DRENES Y PASADAS BAJO RADIER, COMO DUCTO PRESURIZACION, ARMAR RADIER CON D.M. ACMA C-1.39 o D.M.ø8a15.

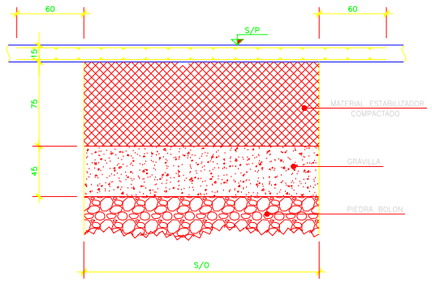

POSICION A DEFINIR SEGUN OBRA

DETALLE DRENES
ESCALA 1:20

DET. 7

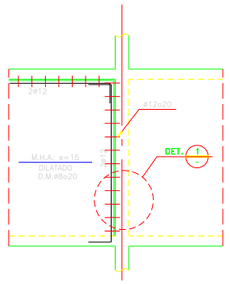

(ESPESOR SEGUN PLANTAS)

DETALLE MURO NO ESTRUCTURAL
SIN ESCALA

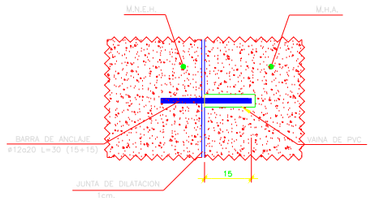

DETALLE 1
ESCALA 1:20

DET. 8

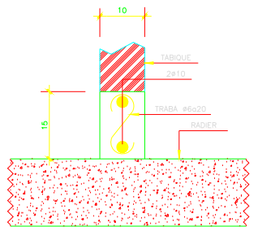

DETALLE ZOCALO APOYO TABIQUE
SIN ESCALA

NOTA: LAS COTAS ENTREPARENTESIS ( ) CORRESPONDEN A LA DIMENSION EN EL EJE DE LA ELEVACION ,Y NO A LA COTA ORTOGONAL INDICADA EN PLANTA.

DET. 9

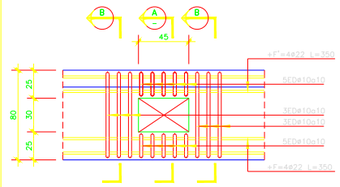

REFUERZO TIP. 1 PASADAS 45x30
ESCALA 1:20

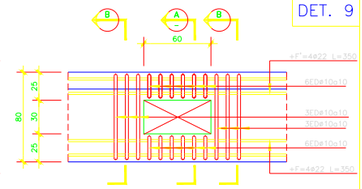

REFUERZO TIP. 3 PASADAS 60x30
ESCALA 1:20

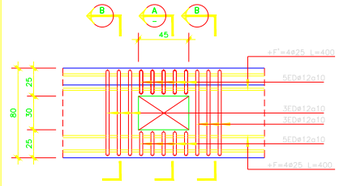

REFUERZO TIP. 2 PASADAS 45x30
ESCALA 1:20

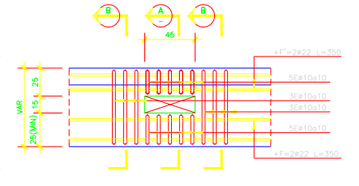

REFUERZO TIP. 4 PASADAS 45x15
ESCALA 1:20

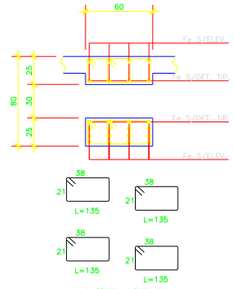

CORTE A
ESCALA 1:20

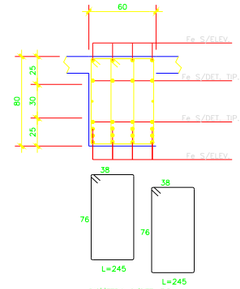

CORTE B
ESCALA 1:20

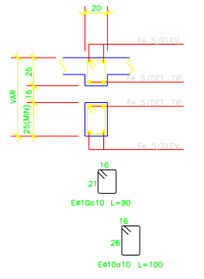

CORTE C
ESCALA 1:20

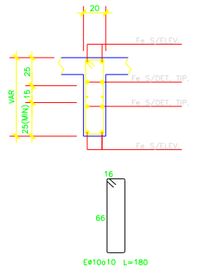

CORTE D
ESCALA 1:20

ESTADO:	APROBADO PARA:
EN DESARROLLO / PRELIMINAR	PROPUESTA X / CONSTRUCCION

Nº	REVISION	ING. / DIB.	FECHA
A	SE EMITE PARA PROPUESTA	JUC/EMF	22/02/2017

MAGDALENA 140 Piso 24 OF.2402 LAS CONDES
SANTIAGO, CHILE | FONO: +56 2 25941300
info@renelagos.com | www.renelagos.com
renelagos engineers

PROYECTO: U. DE LOS ANDES

CONTENIDO: PLANO DE DETALLES TIPICOS

RENE LAGOS CONTRERAS
MARIANNE KUPFER CAUTY
GONZALO ARIAS ESPARZA
LUIS DE LA FUENTE MARTINEZ
SIMON SARNUEZA TORNEALBA

CALCULO	DIBUJO	ESCALAS	NUMERO	REV.
C. MOLINA C.	A. ROCHA B.	INDICADAS	2017_67-002	A
DISEÑO: A. ROCHA B.	REVISO: M. KUPFER C.	FECHA: DICIEMBRE 2017		