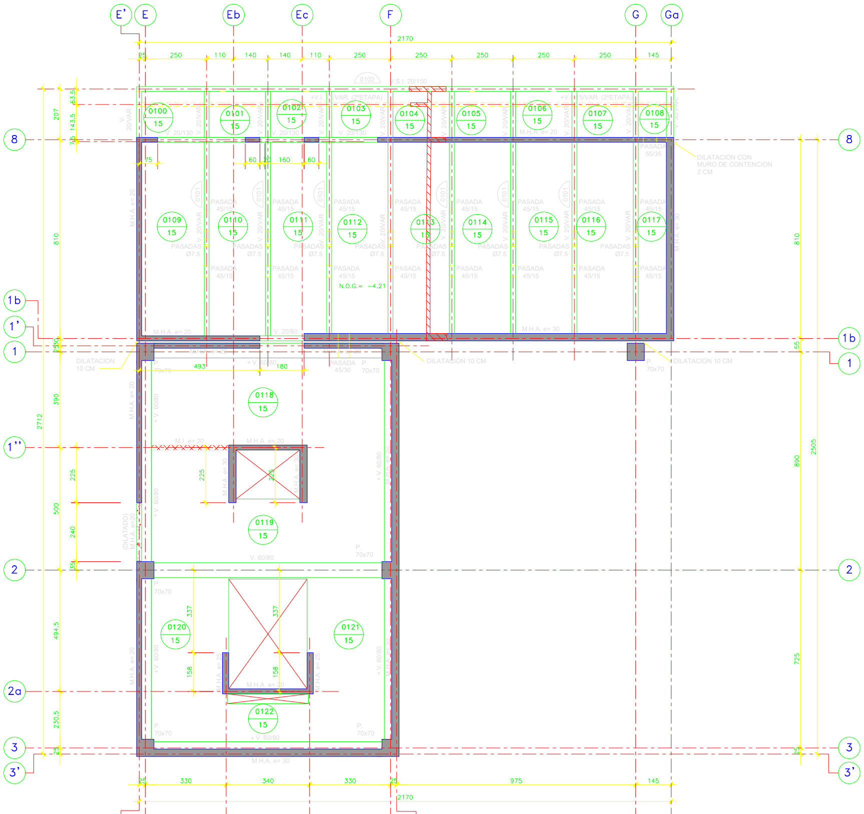

(LOSA e=15 (S.I.C.))
(NIVEL SUPERIOR LOSA -4.01 (S.I.C.))

PLANTA CIELO 1° SUBTERRANEO

ESCALA 1:75

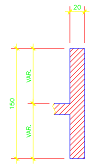

V.S.I. 20/150

ESCALA 1:25

CUADRO DE CONTRAFLECHAS

LOSA	CONTRAFLECHA (cm.)
0100	–
0101	–
0102	–
0103	–
0104	–
0105	–
0106	–
0107	–
0108	–
0109	1.5
0110	1.5
0111	1.5
0112	1.5
0113	1.5
0114	1.5
0115	1.5
0116	1.5
0117	1.5
0118	0.5
0119	0.5
0120	–
0121	–
0122	–

CUADRO DE CONTRAFLECHAS

LOSA	CONTRAFLECHA (cm.)
100	0.5
101	–
102	–
103	–
104	1
105	1
106	1
107	1
108	1
109	1
110	0.5
111	1
112	–
113	–
114	0.5
115	0.5
116	0.5
117	0.5

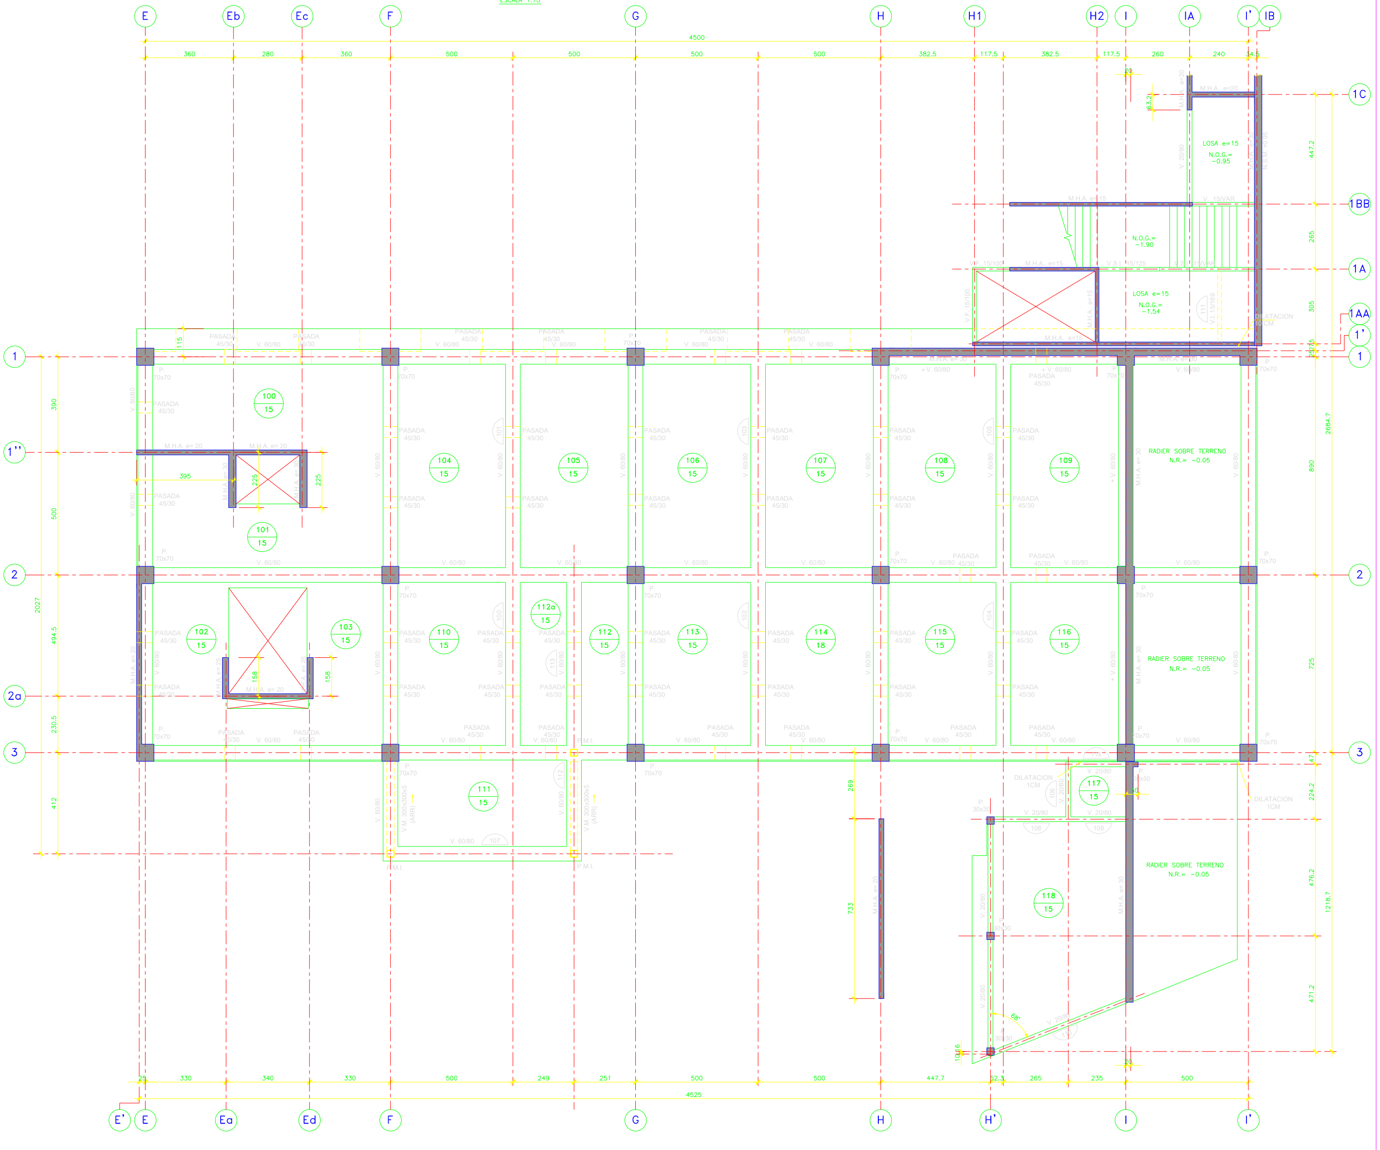

(LOSA e=15 (S.I.C.))
(NIVEL SUPERIOR LOSA -0.05)

PLANTA CIELO PISO 1°

ESCALA 1:75

2017_67-101.dwg
Mon 11 Dec 2017 - 07:16pm

N°	REVISION	ING. / DIB.	FECHA
A	SE EMITE PARA PROPUESTA	JMC/EMF	22/02/2018

ESTADO: EN DESARROLLO ☐ PRELIMINAR ☐

APROBADO PARA: PROPUESTA ☒ CONSTRUCCION ☐

renelagos
engineers

MAGDALENA 140 Piso 24 OF.2402 LAS CONDES
SANTIAGO, CHILE | FONO: +56 2 25941300
info@renelagos.com | www.renelagos.com

PROYECTO
U. DE LOS ANDES

CONTENIDO
PLANTA CIELO 2° SUBTERRANEO
PLANTA CIELO 1° SUBTERRANEO

RENE LAGOS CONTRERAS
MARIANNE KUPFER CAUTY
GONZALO ARIAS ESPARZA
LUIS DE LA FUENTE MARTINEZ
SIMON SANHUEZA TORREALBA

CALCULO J. MOLINA C.
DIBUJO A. ROCHA B.
DISEÑO A. ROCHA B.
REVISO M. KUPFER C.
ESCALAS INDICADAS
FECHA DICIEMBRE 2017
NUMERO 2017_67-101
REV. A