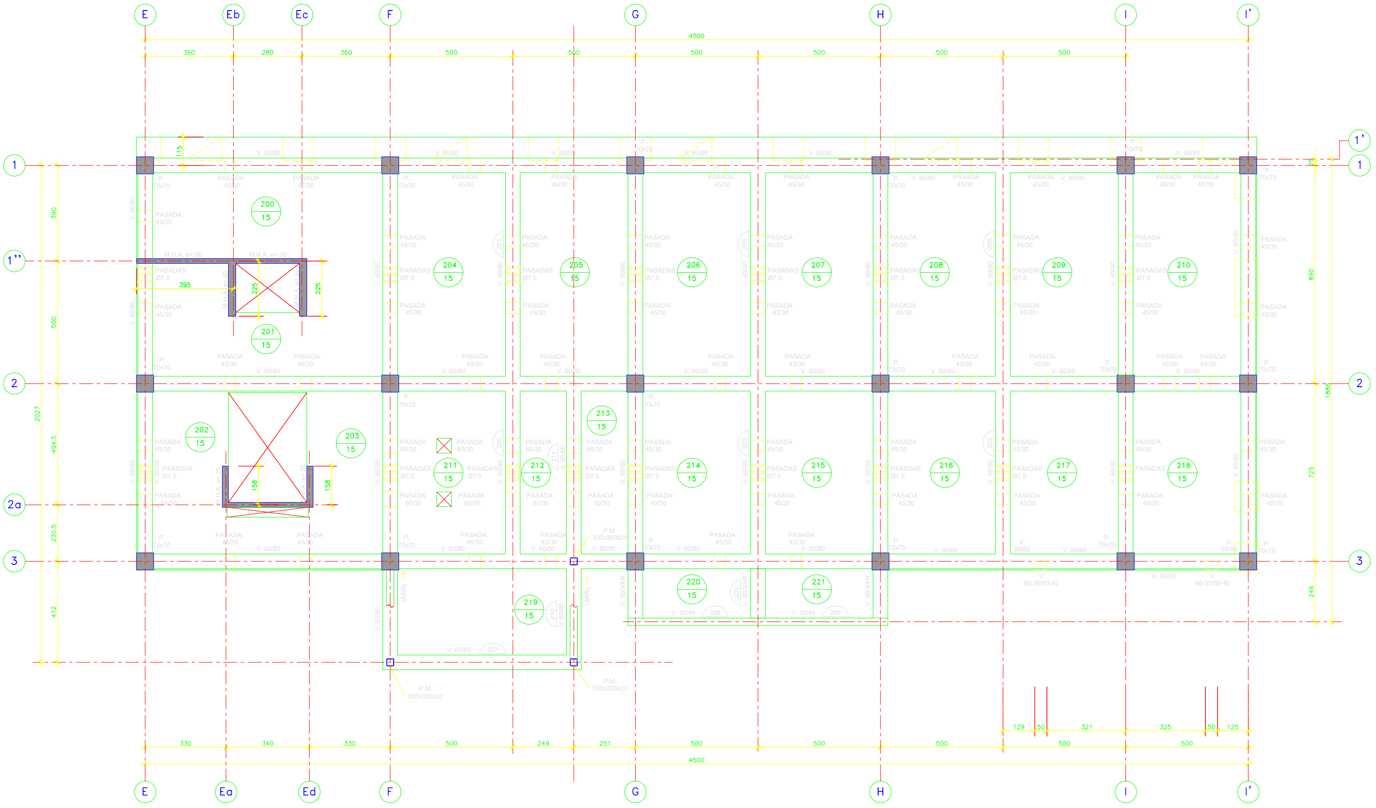

(LOSA e=15 (S.I.C.))
(NIVEL SUPERIOR LOSA +3.91)

PLANTA CIELO PISO 2°

ESCALA 1:75

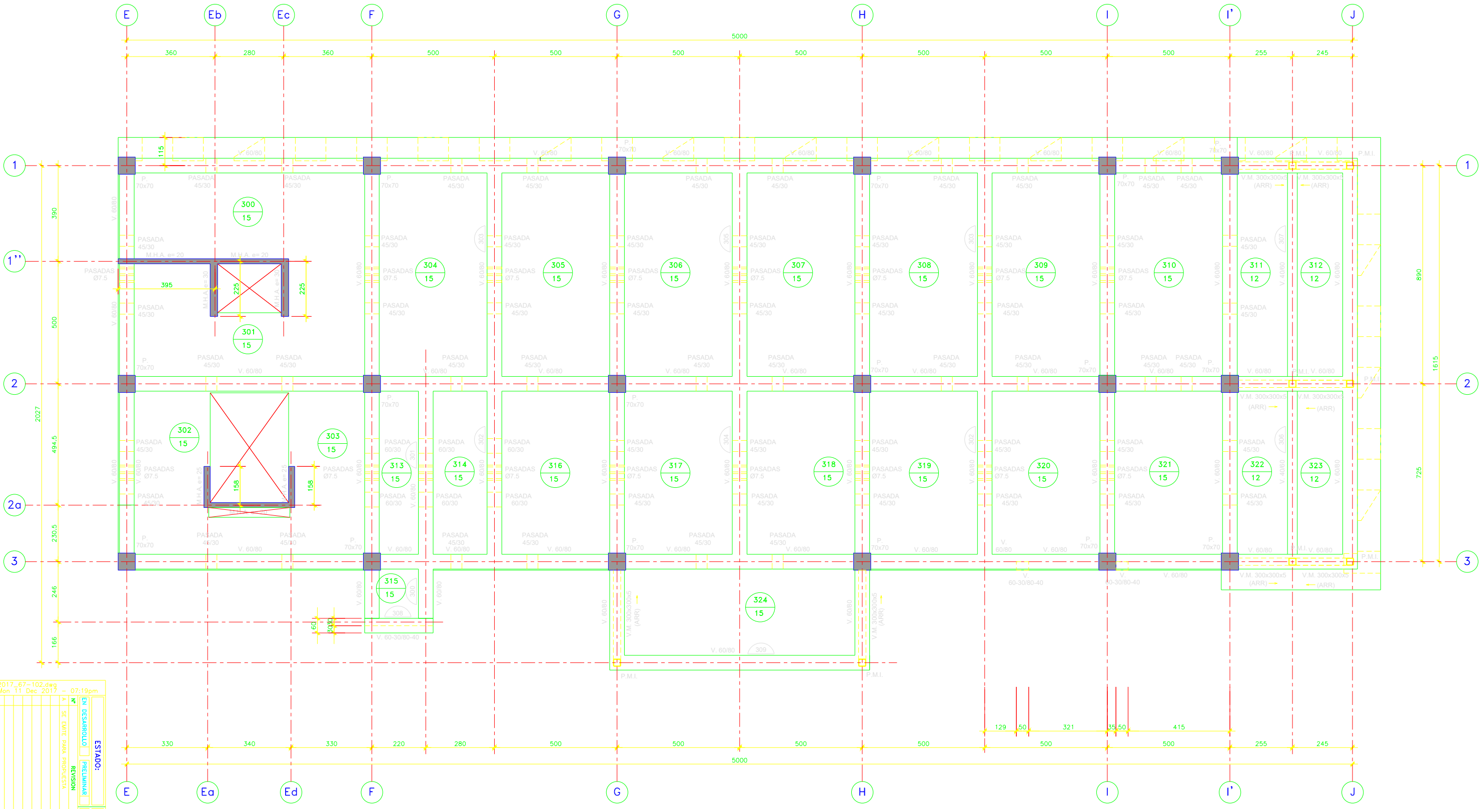

(LOSA e=15 (S.I.C.))
(NIVEL SUPERIOR LOSA +7.87)

PLANTA CIELO PISO 3°

ESCALA 1:75

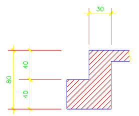

V. 60-30/80-40

ESCALA 1:25

CUADRO DE CONTRAFLECHAS	
LOSA	CONTRAFLECHA (cm.)
200	0.5
201	–
202	–
203	–
204	1
205	1
206	1
207	1
208	1
209	1
210	1
211	0.5
212	–
213	–
214	0.5
215	0.5
216	0.5
217	0.5
218	1
219	1
220	–
221	–

CUADRO DE CONTRAFLECHAS	
LOSA	CONTRAFLECHA (cm.)
300	–
301	–
302	–
303	–
304	1
305	1
306	1
307	1
308	1
309	1
310	1
311	–
312	–
313	–
314	–
315	–
316	0.5
317	0.5
318	0.5
319	0.5
320	0.5
321	0.5
322	–
323	–
324	2

2017_67-102.dwg
Mon 11 Dec 2017 - 07:19pm

ESTADO:
EN DESARROLLO ☐
PRELIMINAR ☐

APROBADO PARA:
PROPUESTA ☒
CONSTRUCCION ☐

N°	REVISION	ING. / DIB.	FECHA
A	SE EMITE PARA PROPUESTA	JMC/EMF	22/02/2018

renelagos engineers

MAGDALENA 140 Piso 24 OF.2402 LAS CONDES
SANTIAGO, CHILE | FONO: +56 2 25941300
info@renelagos.com | www.renelagos.com

RENE LAGOS CONTRERAS
MARIANNE KUPFER CAUTY
GONZALO ARIAS ESPARZA
LUIS DE LA FUENTE MARTINEZ
SIMON SANHUEZA TORREALBA

PROYECTO
U. DE LOS ANDES

CONTENIDO
PLANTA CIELO PISO 1°
PLANTA CIELO PISO 2°

CALCULO J. MOLINA C.
DIBUJO A. ROCHA B.
DISEÑO A. ROCHA B.
REVISO M. KUPFER C.
ESCALAS INDICADAS
FECHA DICIEMBRE 2017
NUMERO 2017_67-102
REV. A