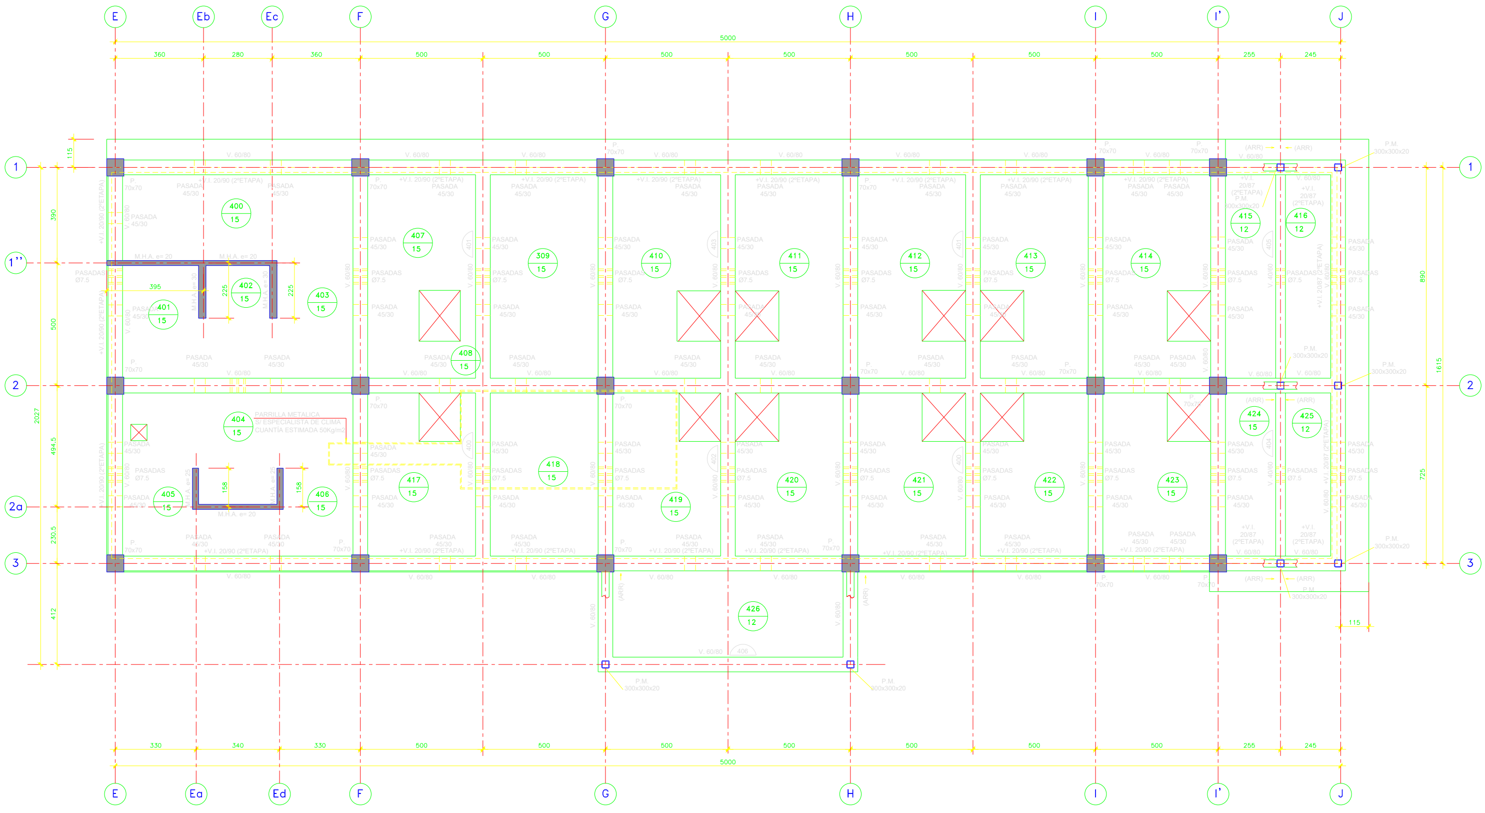

(LOSA e=15 (S.I.C.))
(NIVEL SUPERIOR LOSA +11.83)

PLANTA CIELO PISO 4º

ESCALA 1:75

CUADRO DE CONTRAFLECHAS

LOSA	CONTRAFLECHA (cm.)
400	0.5
401	–
402	–
403	–
404	–
405	–
406	–
407	1
408	0.5
409	1
410	1
411	1
412	1
413	1
414	1
415	0.5
416	0.5
417	0.5
418	1
419	1
420	0.5
421	0.5
422	0.5
423	0.5
424	–
425	–
426	1

2017_67-103.dwg
Mon 11 Dec 2017 - 07:20pm

ESTADO:		APROBADO PARA:	
EN DESARROLLO ☐	PRELIMINAR ☐	PROPUESTA ☒	CONSTRUCCION ☐

Nº	REVISION	ING. / DIB.	FECHA
A	SE EMITE PARA PROPUESTA	JMC/EMF	22/02/2018

MAGDALENA 140 Piso 24 OF.2402 LAS CONDES
SANTIAGO, CHILE | FONO: +56 2 25941300
info@renelagos.com | www.renelagos.com

renelagos
engineers

RENE LAGOS CONTRERAS
MARIANNE KUPFER CAUTY
GONZALO ARIAS ESPARZA
LUIS DE LA FUENTE MARTINEZ
SIMON SANHUEZA TORREALBA

PROYECTO
U. DE LOS ANDES

CONTENIDO
PLANTA CIELO PISO 3º

CALCULO J. MOLINA C.	DIBUJO A. ROCHA B.	ESCALAS INDICADAS	NUMERO 2017_67-103	REV. A
DISEÑO A. ROCHA B.	REVISO M. KUPFER C.	FECHA DICIEMBRE 2017		