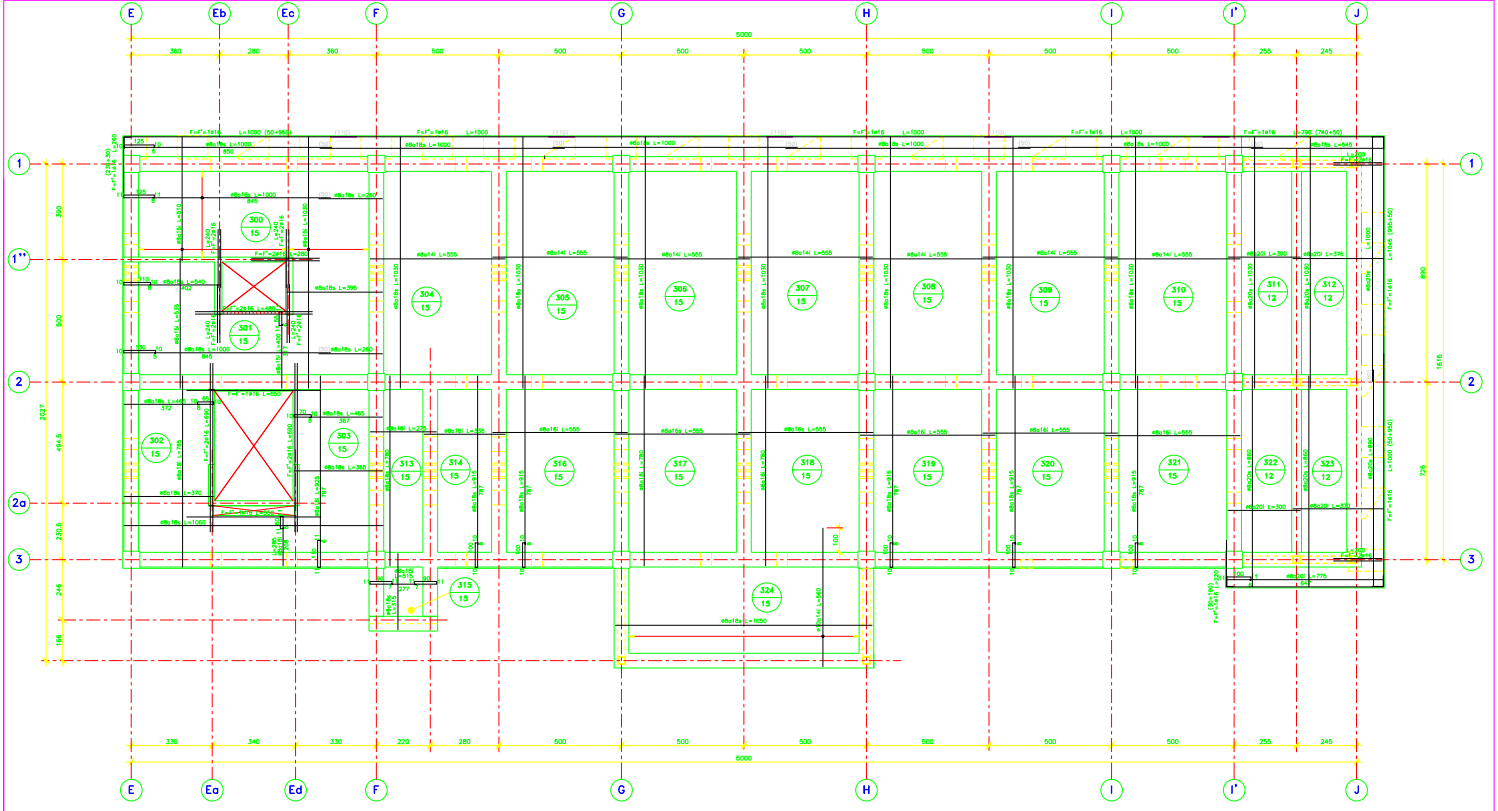

ARMADURA MALLA INFERIOR LOSA CIELO 3° PISO

ESCALA 1:75

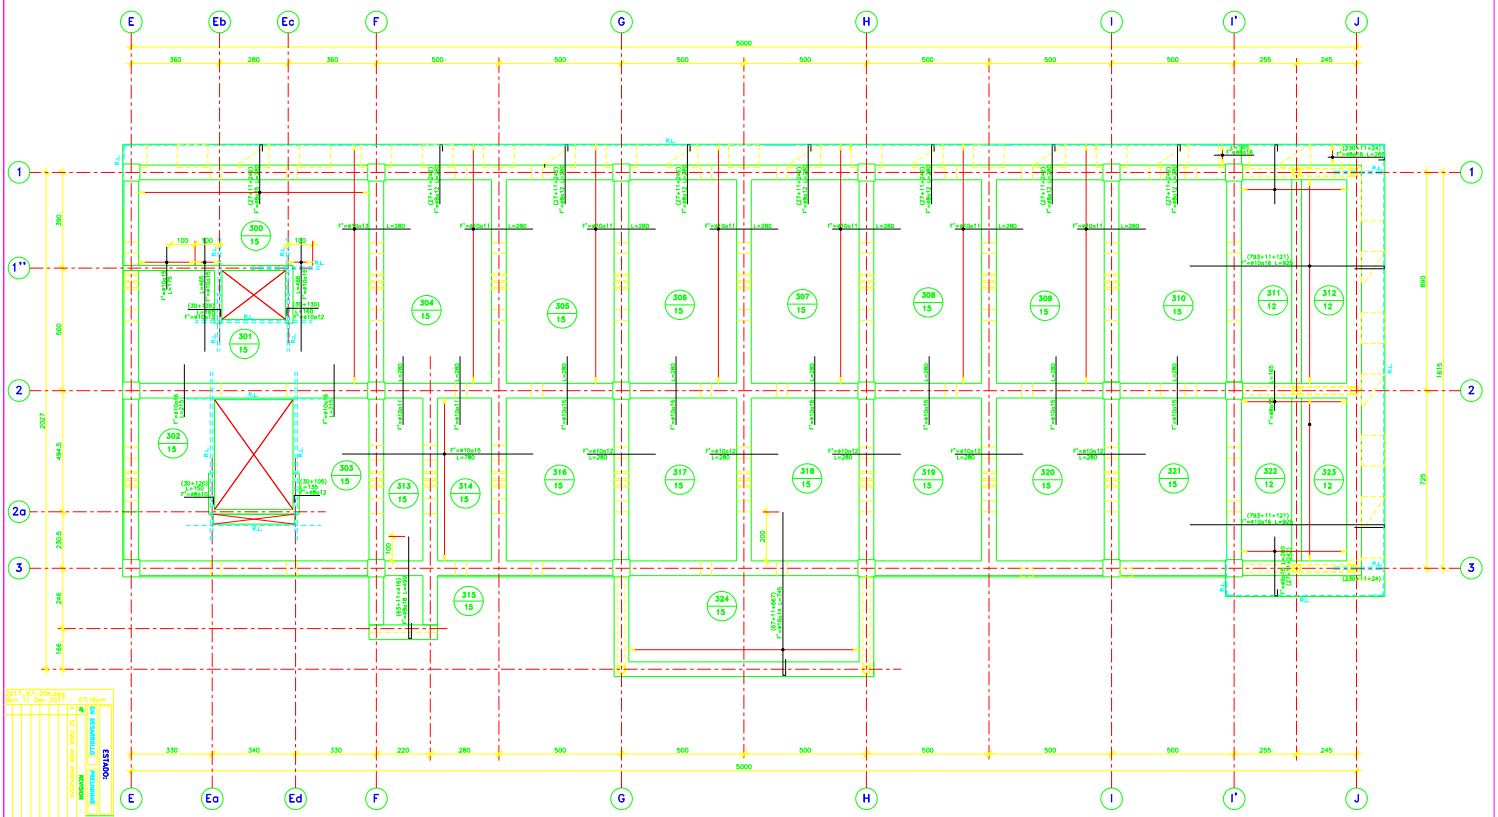

ARMADURA MALLA SUPERIOR LOSA CIELO 3° PISO

ESCALA 1:75

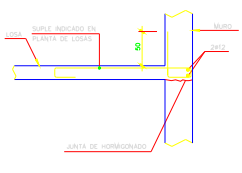

DETALLE ALTERNATIVO SUPLES EN MUROS

ESCALA 1:20

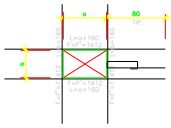

REFUERZO TIP. SHAFT

ESCALA 1:25

(TAMAÑO MAX. 100x100 cm.)

ESTADO: EN DESARROLLO | REVISIÓN | APROBADO PARA: PROPUESTA | CONSTRUCCIÓN

FECHA: 27/04/2018

U. DE LOS ANDES

ARMADURA MALLA INFERIOR LOSA CIELO 3° PISO

2017-67-204

A