



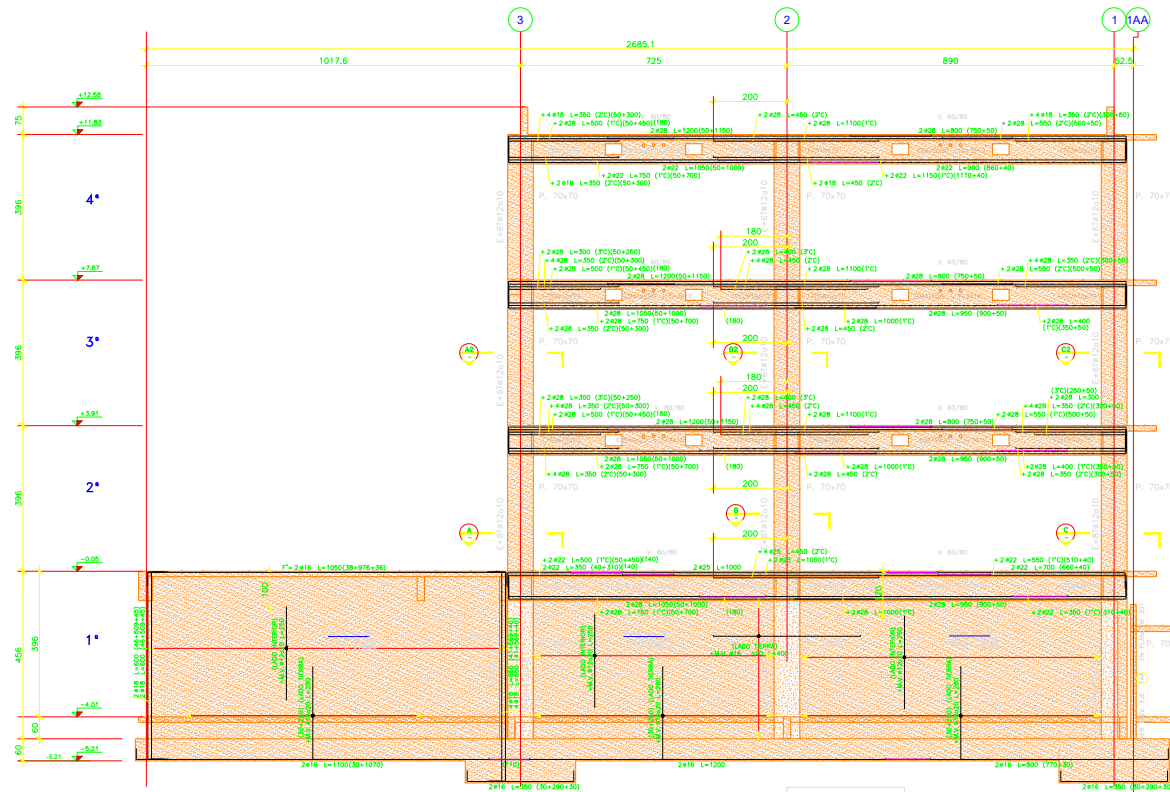

ELEVACION EJE I


ESCALA 1:50

NOTA:
PARA LAS PROYECCIONES EN VISTA
VER REFERENCIAS 1002 Y 1011
DETALLE O PLANO NÚMERO (S.I.C.)

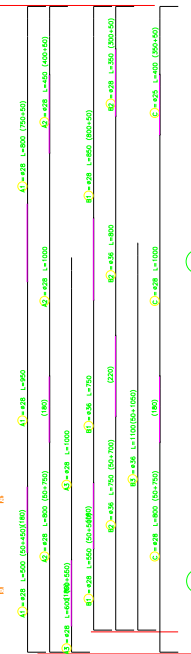


CORTE A2

ESCALA 1:20

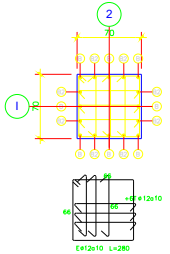


CORTE B2

ESCALA 1:20

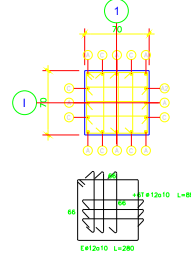


CORTE C2

ESCALA 1:20

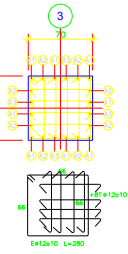


CORTE A

ESCALA 1:20

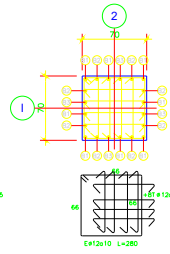

CORTE B

ESCALA 1:20

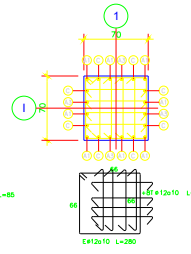

CORTE C

ESCALA 1:20

ESTADO		APROBADO PARA:	
ELABORADO	PROYECTADO	PROYECTADO	PROYECTADO
REVISADO	REVISADO	REVISADO	REVISADO
SE ENTREGA PARA PROYECTO	SE ENTREGA PARA PROYECTO	SE ENTREGA PARA PROYECTO	SE ENTREGA PARA PROYECTO
FECHA: 22/10/2017		FECHA: 22/10/2017	
PROYECTO		PROYECTO	
U. DE LOS ANDES		U. DE LOS ANDES	
ELEVACION EJE I		ELEVACION EJE I	
AUTOR: RENELAGOS		AUTOR: RENELAGOS	
REVISOR: RENELAGOS		REVISOR: RENELAGOS	
SUPERVISOR: RENELAGOS		SUPERVISOR: RENELAGOS	
FECHA: 2017		FECHA: 2017	