

ARMADURA MALLA INFERIOR LOSA CIELO 1° SUBTERRANEO


ESCALA 1:7E

DETALLE ALTERNATIVO SUPLES EN MUROS

ESCALA 1:20

REFUERZO TIP. SHAFT

ESCALA 1:25
(TAMARCO MÁX. 100x100 cm.)

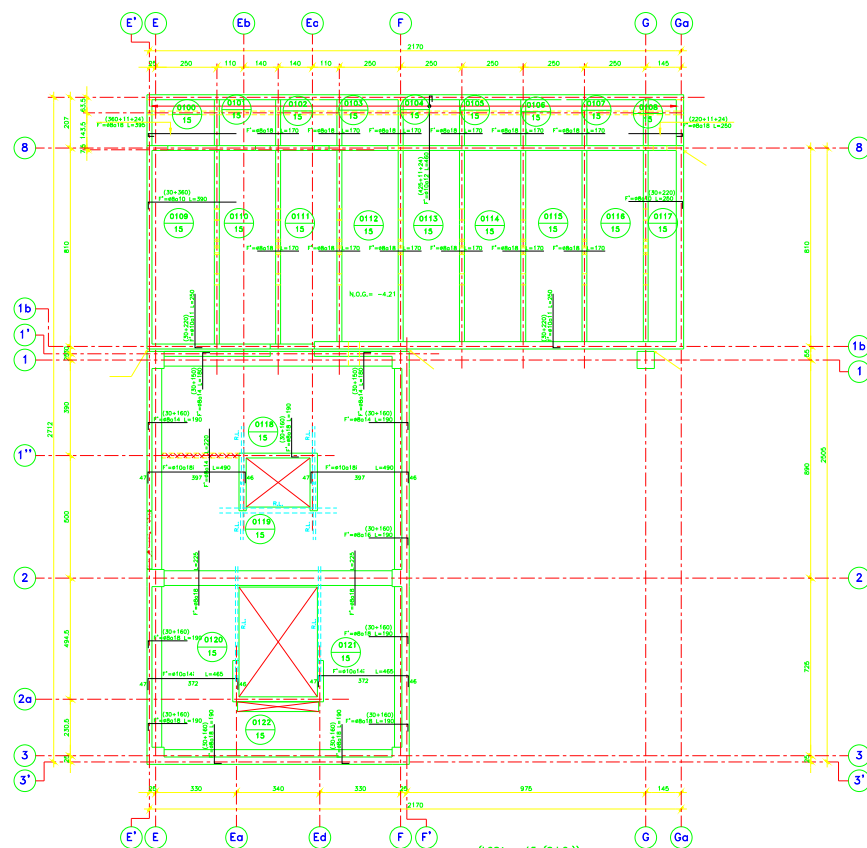

ARMADURA MALLA SUPERIOR LOSA CIELO 1° SUBTERRANEO

ESCALA 1:75

[illegible]