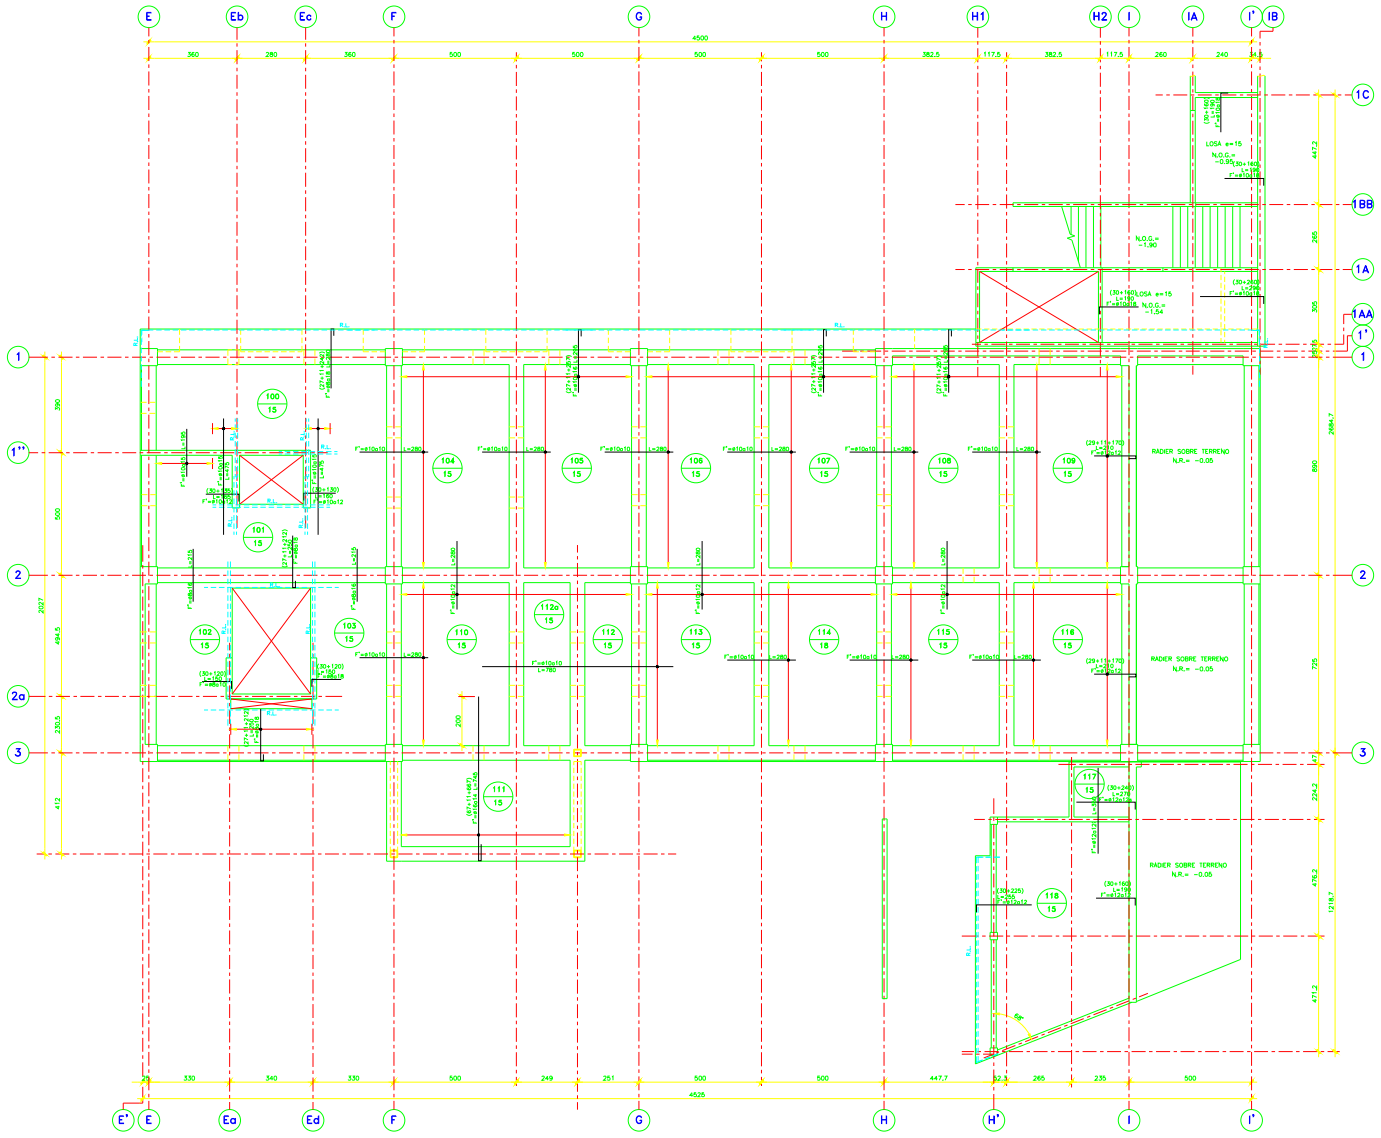

ARMADURA MALLA SUPERIOR LOSA CIELO 1° PISO

ESCALA 1:75

DETALLE ALTERNATIVO SUPLES EN MUROS

ESCALA 1:20

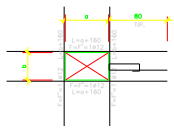

REFUERZO TIP. SHAFT

ESCALA 1:25

(TAMAÑO MAX. 100x100 cm.)

PROYECTO	U. DE LOS ANDES
CONTIENE	ARMADURA MALLA SUPERIOR LOSA CIELO 1° PISO
ESCALA	1:75
FECHA	2017_07-202-S1
REV.	A

ESTADO: EN DESARROLLO / PRELIMINAR / PROPUESTA X / APROBADO PARA CONSTRUCCIÓN

FECHA: 07/16

INGENIERIA Y PROYECTOS SANTIAGO, CHILE | FONO: +56 2 2264 0300
www.rentelagos.com