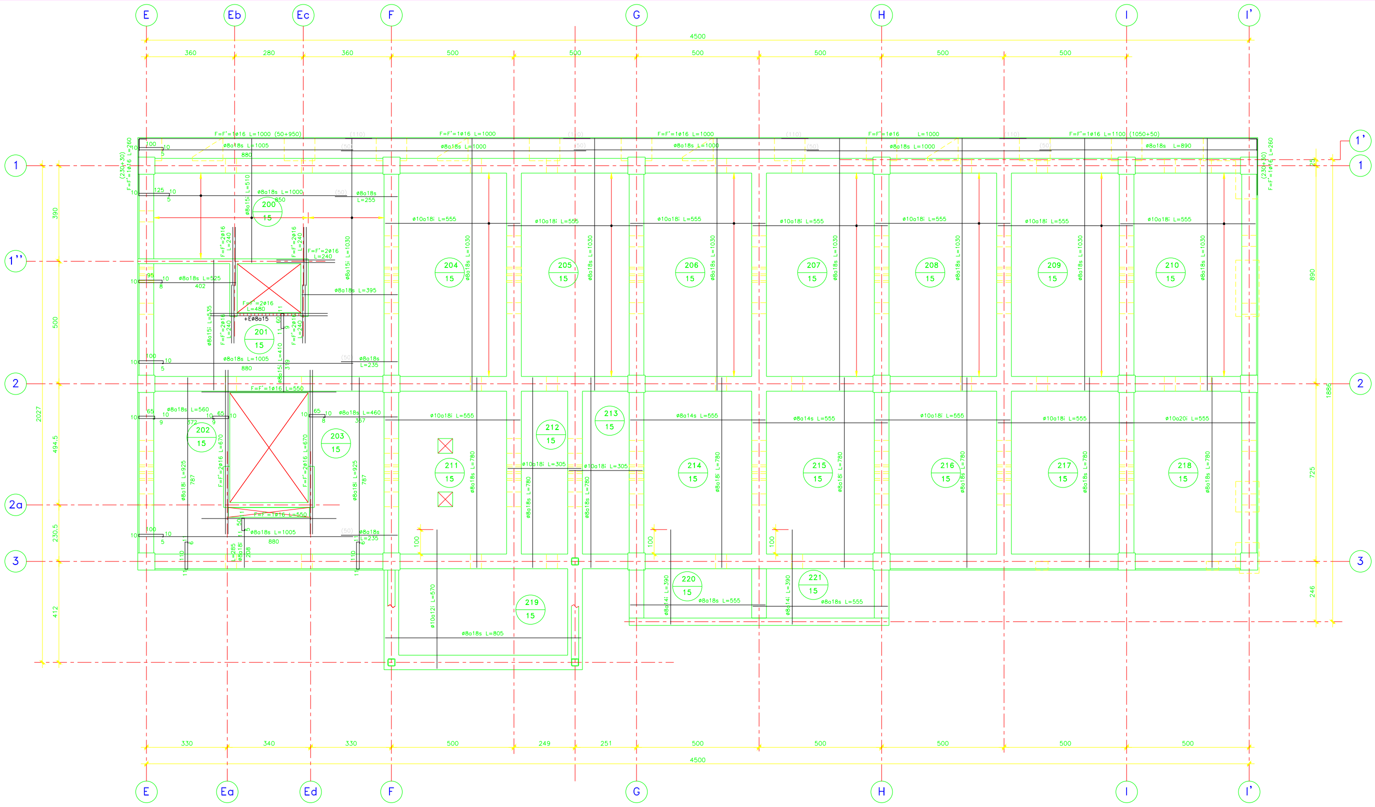

ARMADURA MALLA INFERIOR LOSA CIELO 2° PISO

ESCALA 1:75

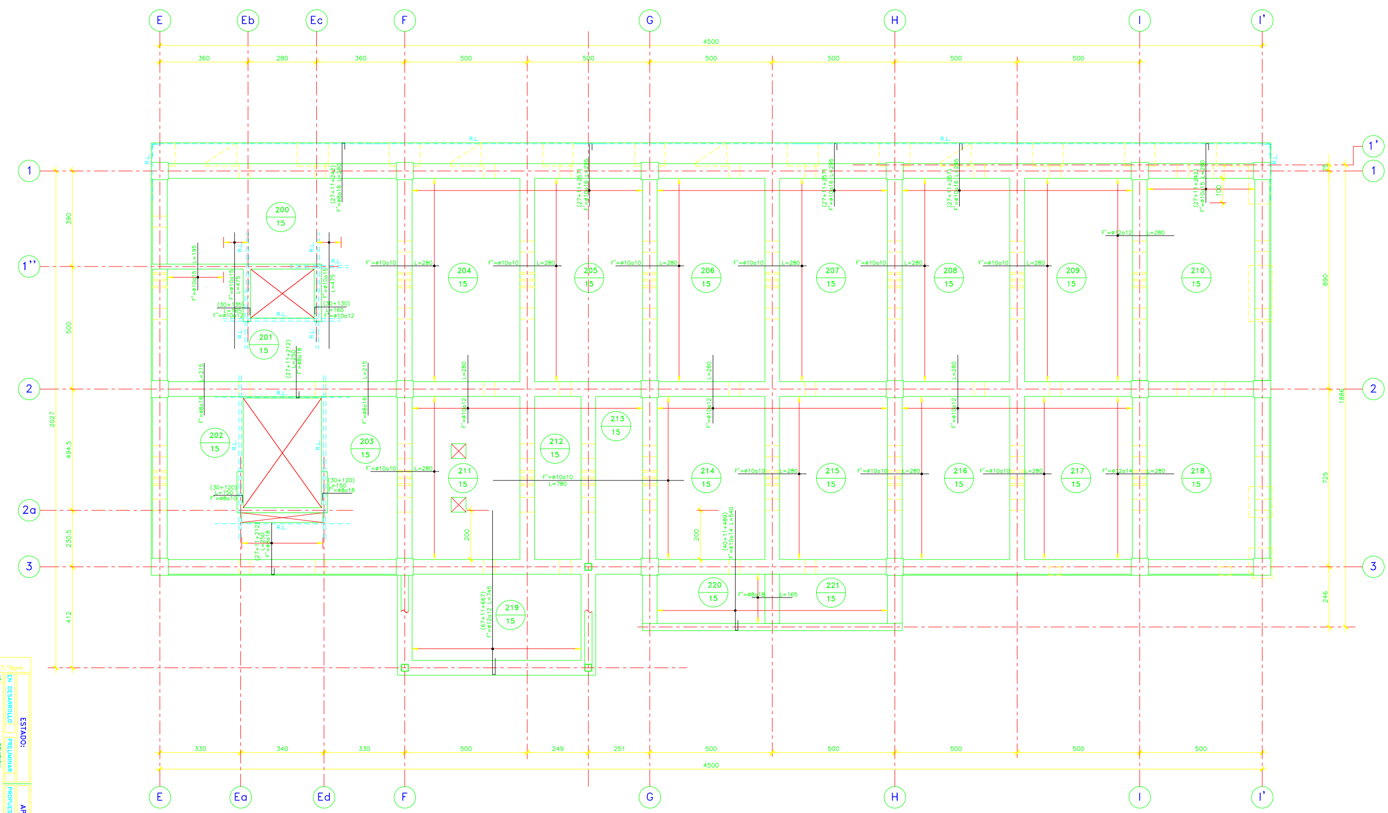

ARMADURA MALLA SUPERIOR LOSA CIELO 2° PISO

ESCALA 1:75

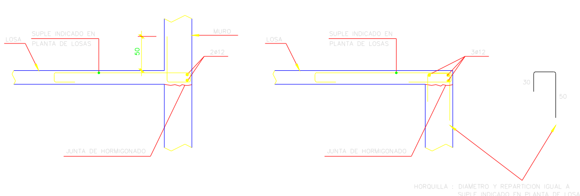

DETALLE ALTERNATIVO SUPLES EN MUROS

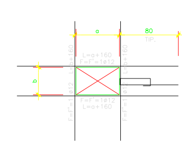

REFUERZO TIP. SHAFT

ESTADO:

APROBADO PARA: PROPUESTA X CONSTRUCCION

ING. / DIB.	FECHA
JMC/EMF	22/02/2018

renelagos engineers

MAGDALENA 140 Piso 24 OF.2402 LAS CONDES
SANTIAGO, CHILE | FONO: +56 2 25941300
info@renelagos.com | www.renelagos.com

RENE LAGOS CONTRERAS
MARIANNE KUPFER CAUTY
GONZALO ARIAS ESPARZA
LUIS DE LA FUENTE MARTINEZ
SIMON SANHUEZA TORREALBA

PROYECTO: U. DE LOS ANDES

CONTENIDO: ARMADURA MALLA INF. Y SUP. LOSA CIELO 2° PISO

CALCULO	DIBUJO	ESCALAS
J. MOLINA C.	E. MORALES F.	INDICADAS

DISEÑO	REVISO	FECHA
E. MORALES F.	M. KUPFER C.	DICIEMBRE 2017

NUMERO: 2017_67-203 REV.: A