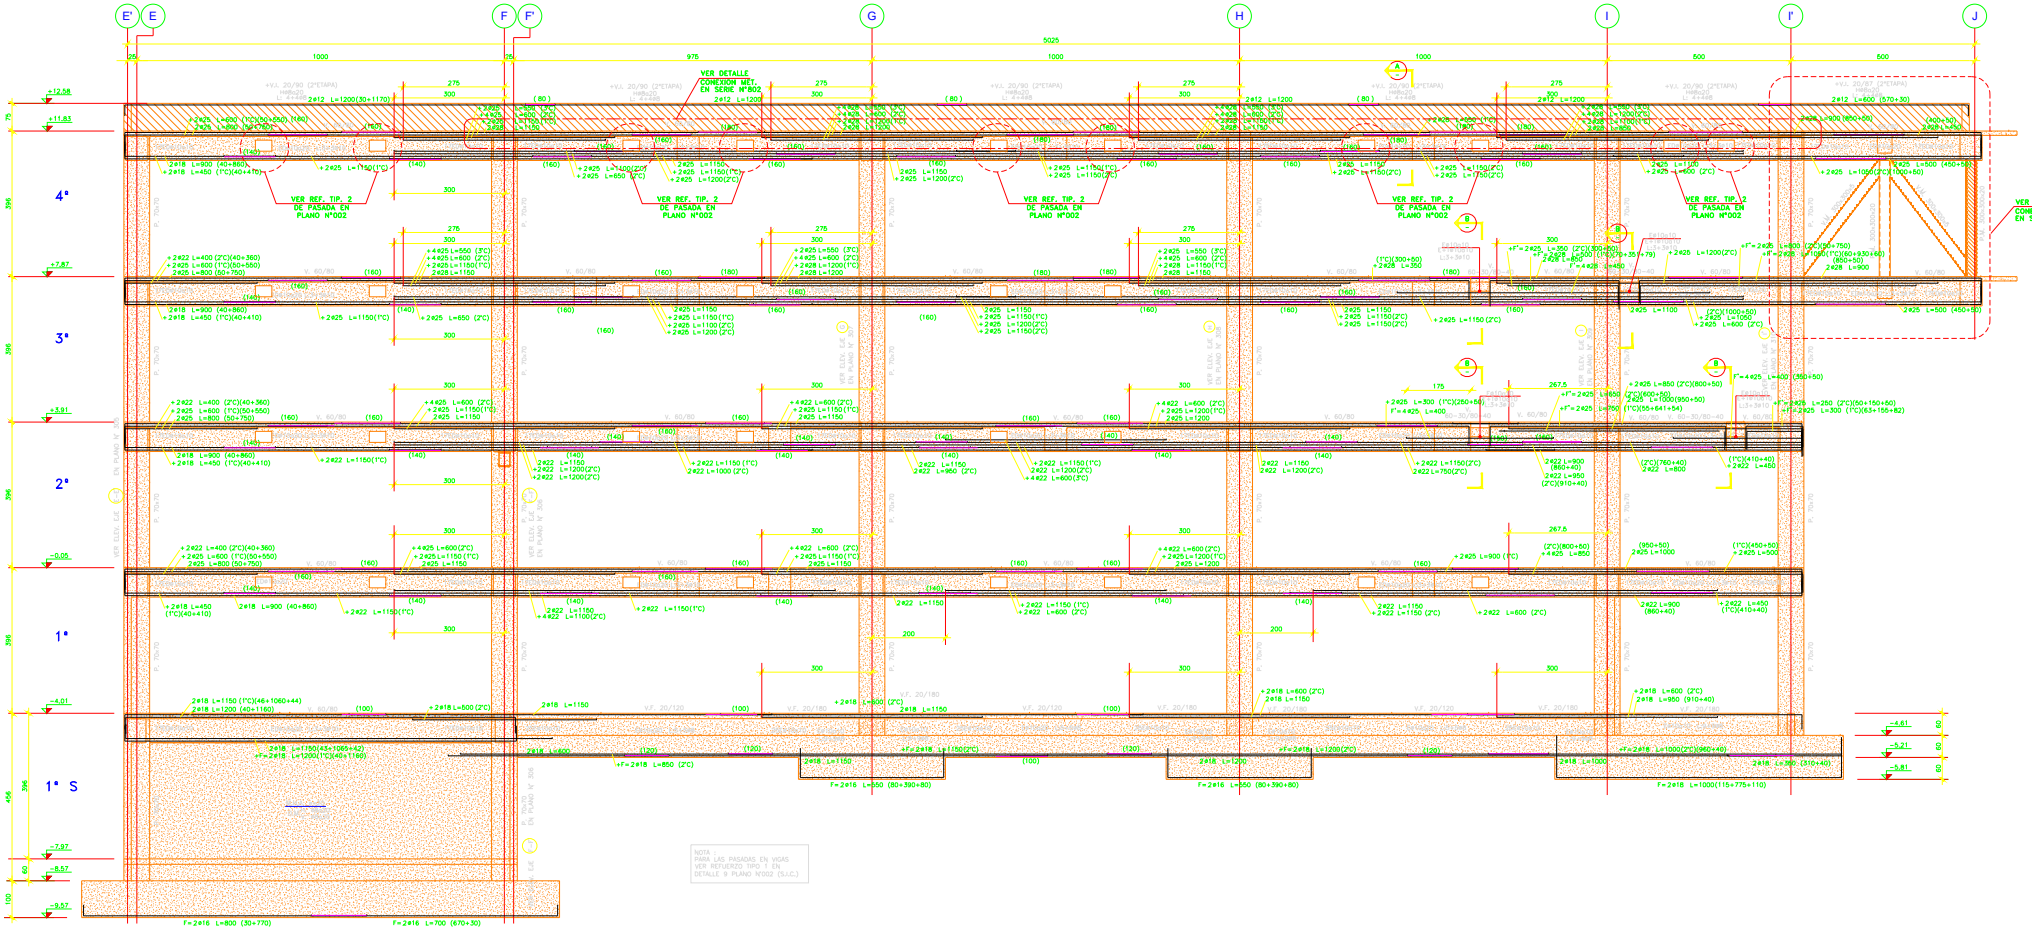

ELEVACION EJE 3-3'

ESCALA 1:50

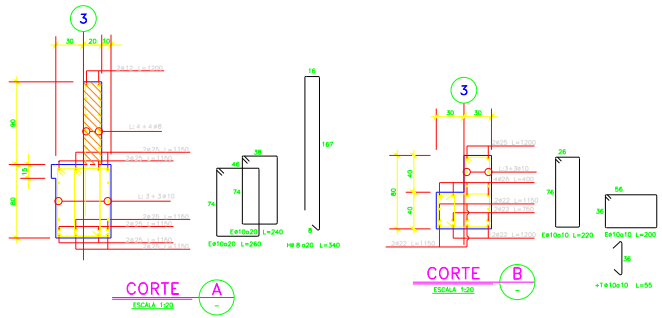

ESTADO:		APROBADO PARA:	
EN DESARROLLO	PRELIMINAR	PROPUESTA X	CONSTRUCCION

Nº	REVISION	IND. / DIB.	FECHA
A	SE EMITE PARA PROPUESTA	JAC / TM	22/02/2017

MAGDALENA 140 Piso 24 OF.2402 LAS CONDES
SANTIAGO, CHILE | FONO: +56 2 25841300
info@renelagos.com | www.renelagos.com
renelagos

PROYECTO: U. DE LOS ANDES

CONTENIDO: ELEVACION EJE 3-3'

CALCULO:	DIBUJO: MORALES J.	ESCALA: 1:50	FECHA:
DISEÑO:	REVISO:	FECHA: MAY 2017	2017_67-303

REV: A