
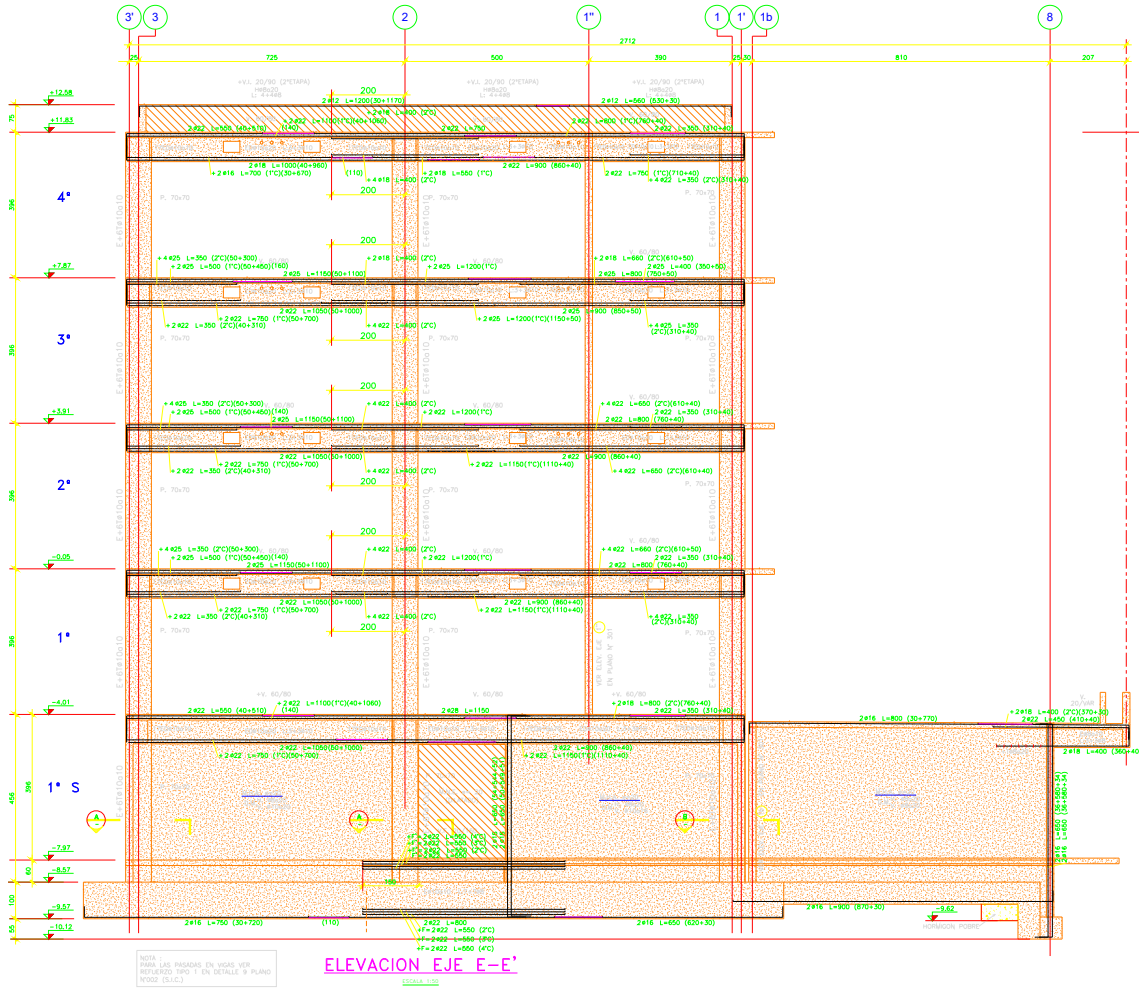



ELEVACION EJE E-E'

ESCALA 1:50

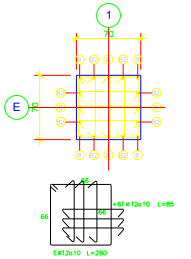


CORTE B

ESCALA 1:20

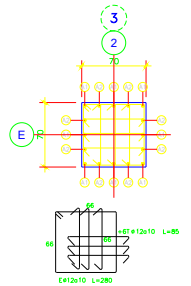


CORTE A

ESCALA 1:20

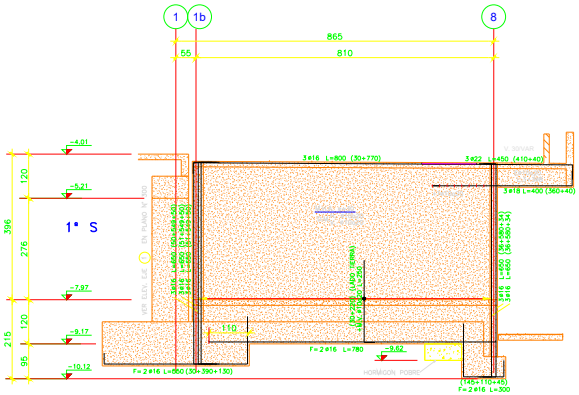

ELEVACION EJE Ga

ESCALA 1:50

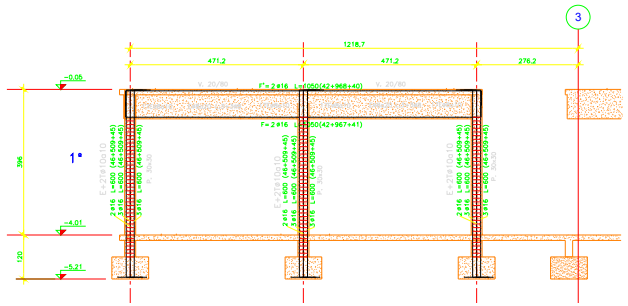

ELEVACION EJE H'

ESCALA 1:50

ESTADO:		APROBADO PARA:	
EN DESARROLLO	PRELIMINAR	PROPUESTA X	CONSTRUCCION
N°	REVISION	IND. / DEL.	FECHA
1	SE EMITE PARA PROPUESTA	ACUTM	22/12/2017

MAGDALENA 140 Piso 24 OF.2402 LAS CONDES
SANTIAGO, CHILE | FONO: +56 2 25841300
info@renelagos.com | www.renelagos.com

renelagos

PROYECTO: U. DE LOS ANDES

CONTENIDO: ELEVACION EJE E-E', H', Ga

DISEÑO	DIBUJO	ESCALA	FECHA	PLANO	REV.
MOLINA C.	MORALES J.	INDICADA	DICIEMBRE 2017	2017_67-305	A
MORALES J.	REVISO	DUPERT A.			