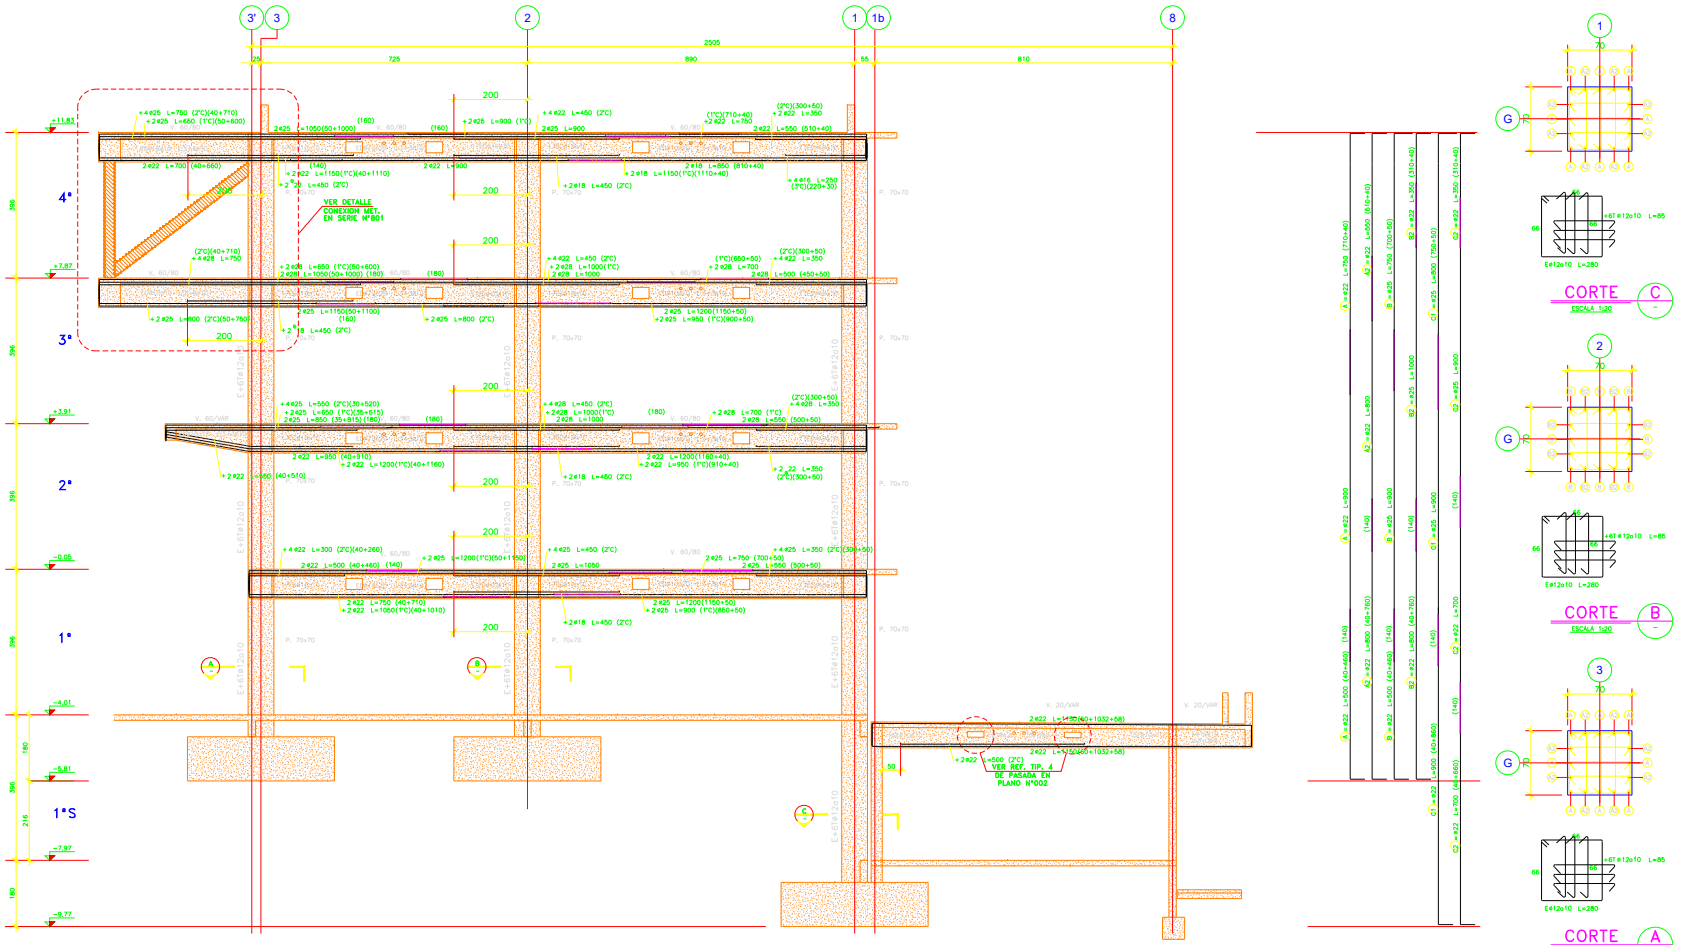

ELEVACION EJE G

ESCALA 1:50

ESTADO:			APROBADO PARA:		
EN DESARROLLO	PRELIMINAR	PROPUESTA X	CONSTRUCCION		
N°	REVISION		IND. / DIB.	FECHA	
A	SE EMITE PARA PROPUESTA		JAC / TM	22/12/2017	

MAGDALENA 140 Piso 24 OF.2402 LAS CONDES
SANTIAGO, CHILE | FONO: +56 2 25841300
info@renelagos.com | www.renelagos.com

renelagos

PROYECTO: U. DE LOS ANDES

CONTENIDO: ELEVACION EJE G

CALCULO	DIBUJO	ESCALA	PROYECTO	REV.
MOLINA C.	MORALES J.	1:50	2017_67-307	A
DISEÑO	REVISO	FECHA		
MORALES J.	SUPERF. AC.	DICIEMBRE 2017		